



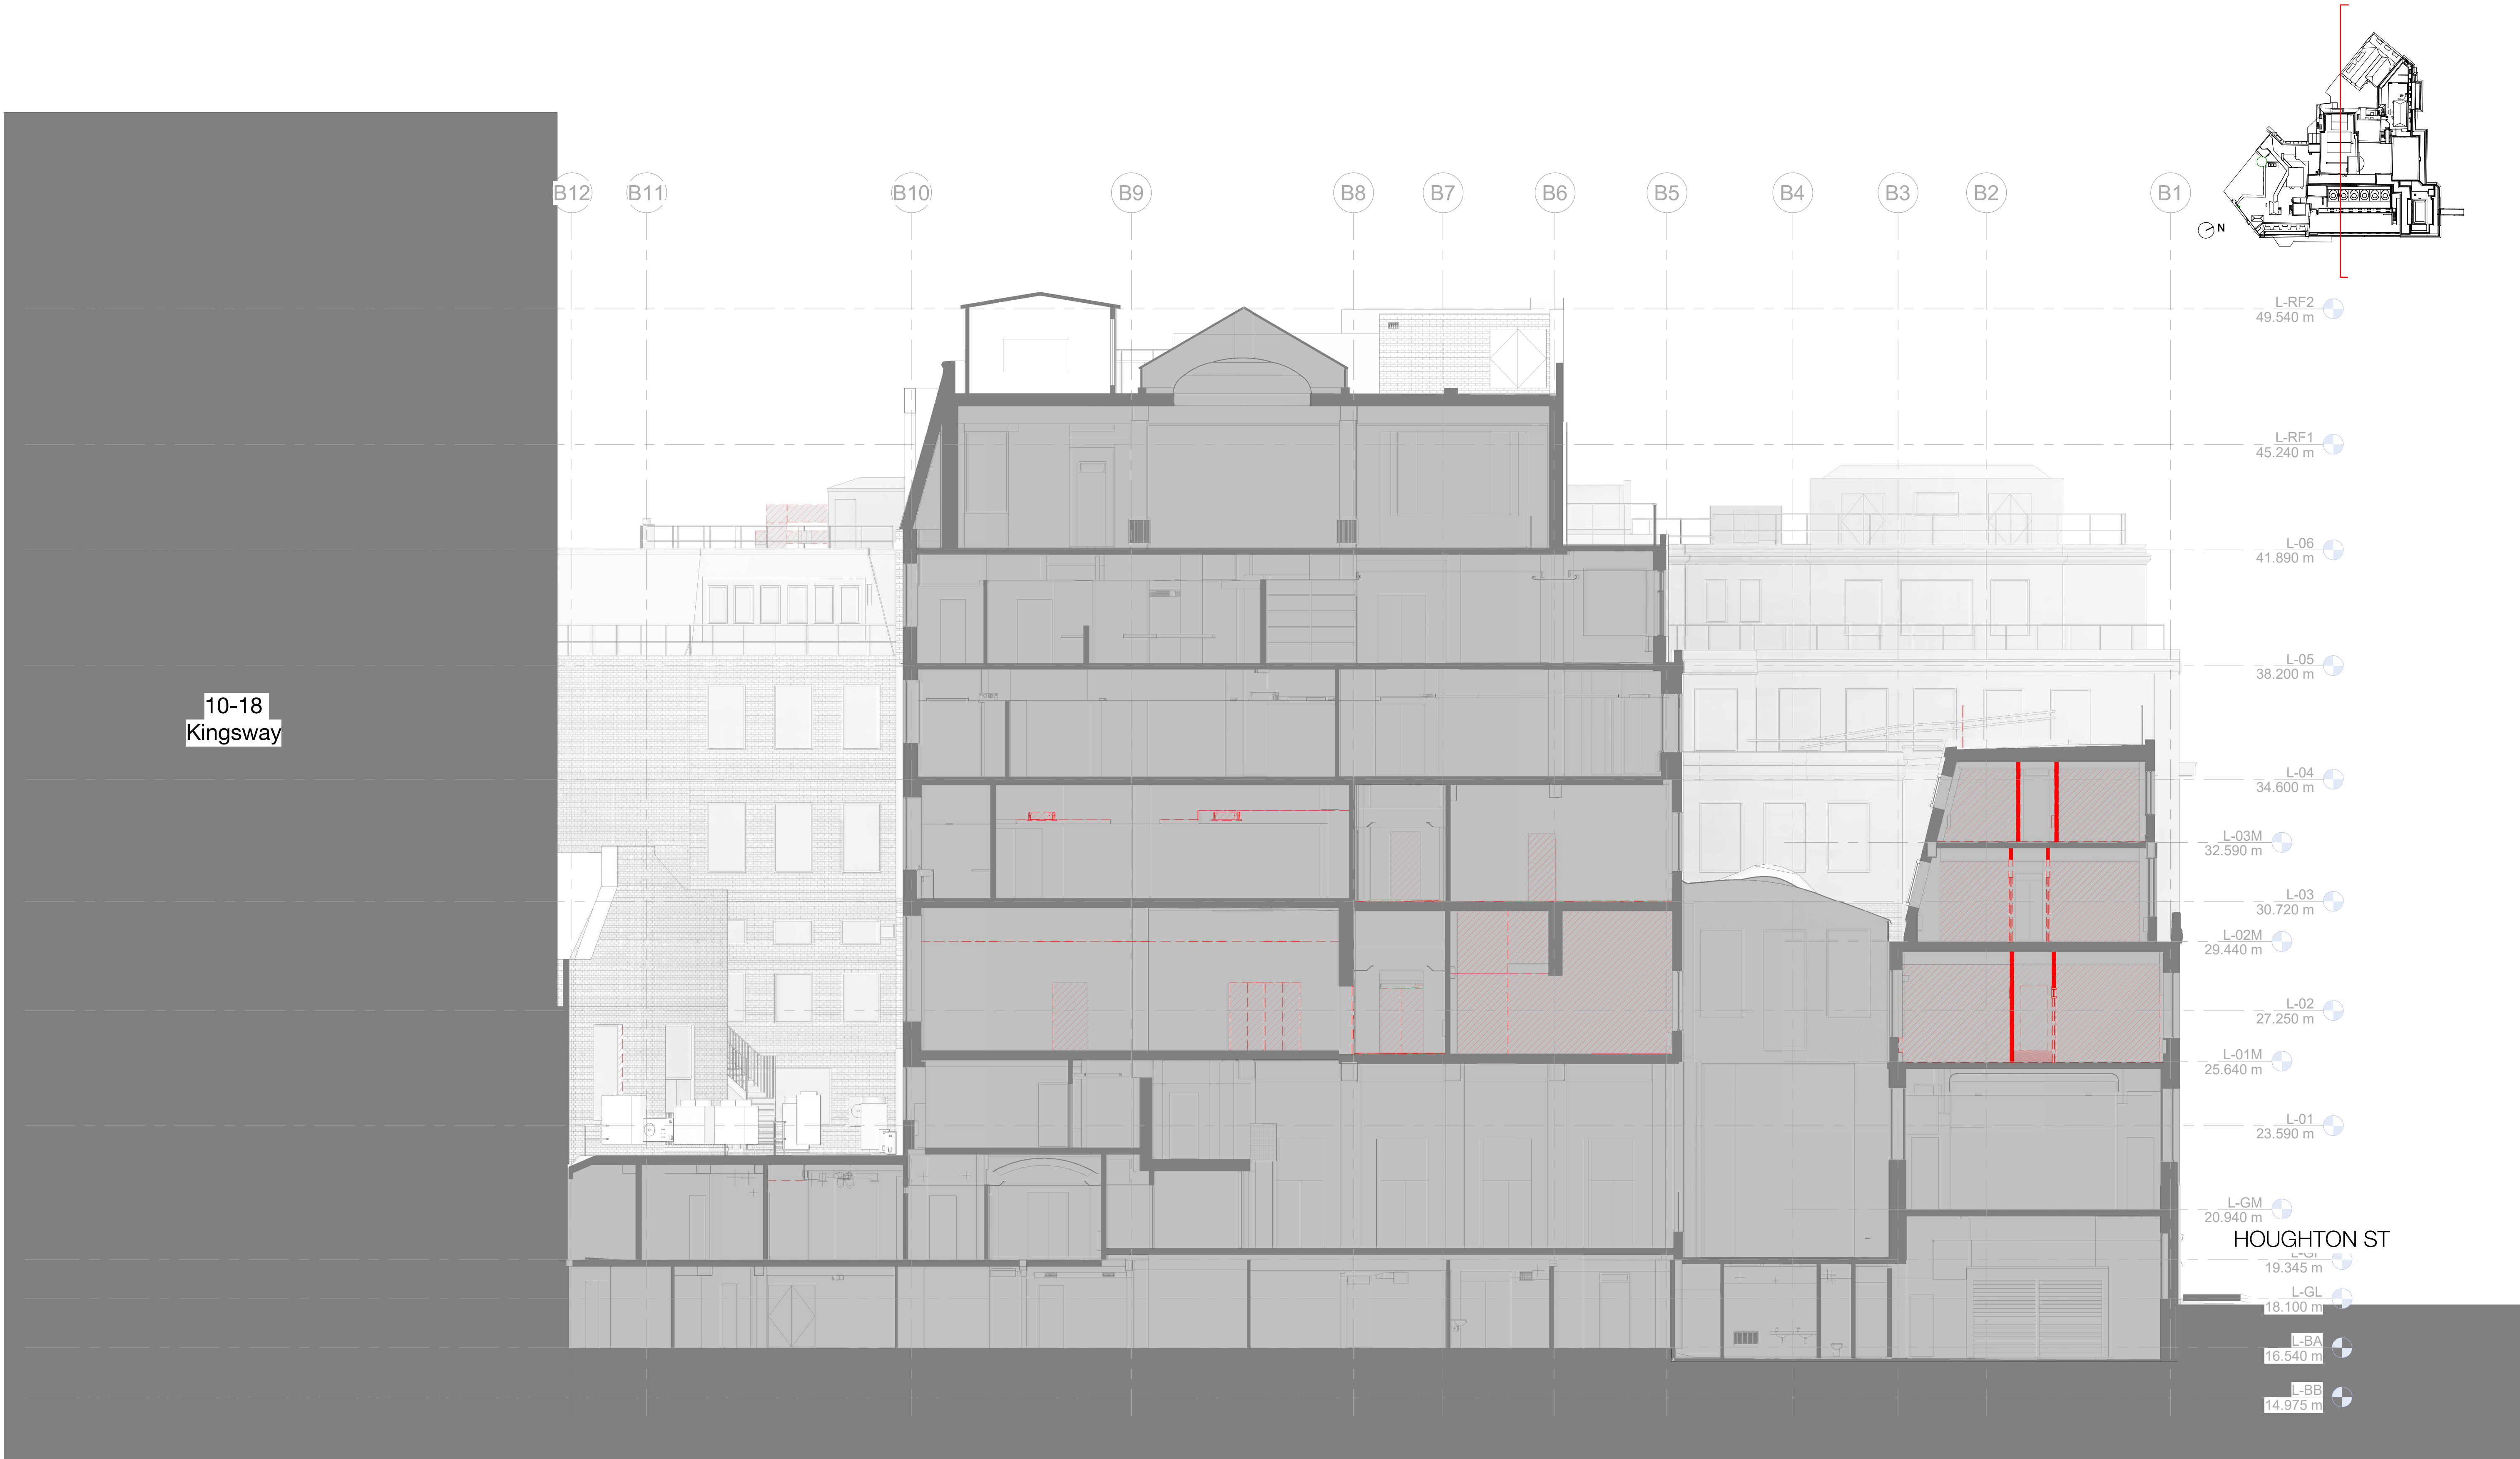

Section AA - Existing & Strip-out
1 : 100

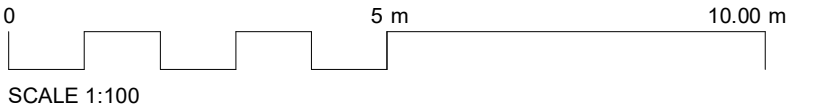

Rev		Description	Date						
P1		Planning	07.12.22						
Copyright Hawkins\Brown Architects No implied licence exists. This drawing should not be used to calculate areas for the purposes of valuation. Do not scale this drawing. All dimensions to be checked on the site by the contractor and such dimensions to be their responsibility. All work must comply with relevant British Standards and Building Regulations requirements. Drawing errors and omissions to be reported to the architect. To be read in conjunction with Architect's specification and other consultant information.						To be Stripped Out			
				Scale @ A1		Date	Job Number	Project LSE Old Building Refurbishment Houghton St London WC2A 2AE UK	
				As indicated		07/12/22	210224		
				Drawn By		Checked By	Status	Drawing Existing / Strip Out Section AA	
				CG		RG	S2		
Drawing No.		Rev	Purpose of Issue						
LSEOLD-HBA-V1-XX-DR-A-080300		P1	For Information						

159 St John Street
London EC1V 4QJ
mail@hawkinsbrown.com
hawkinsbrown.com

Hawkins\Brown