


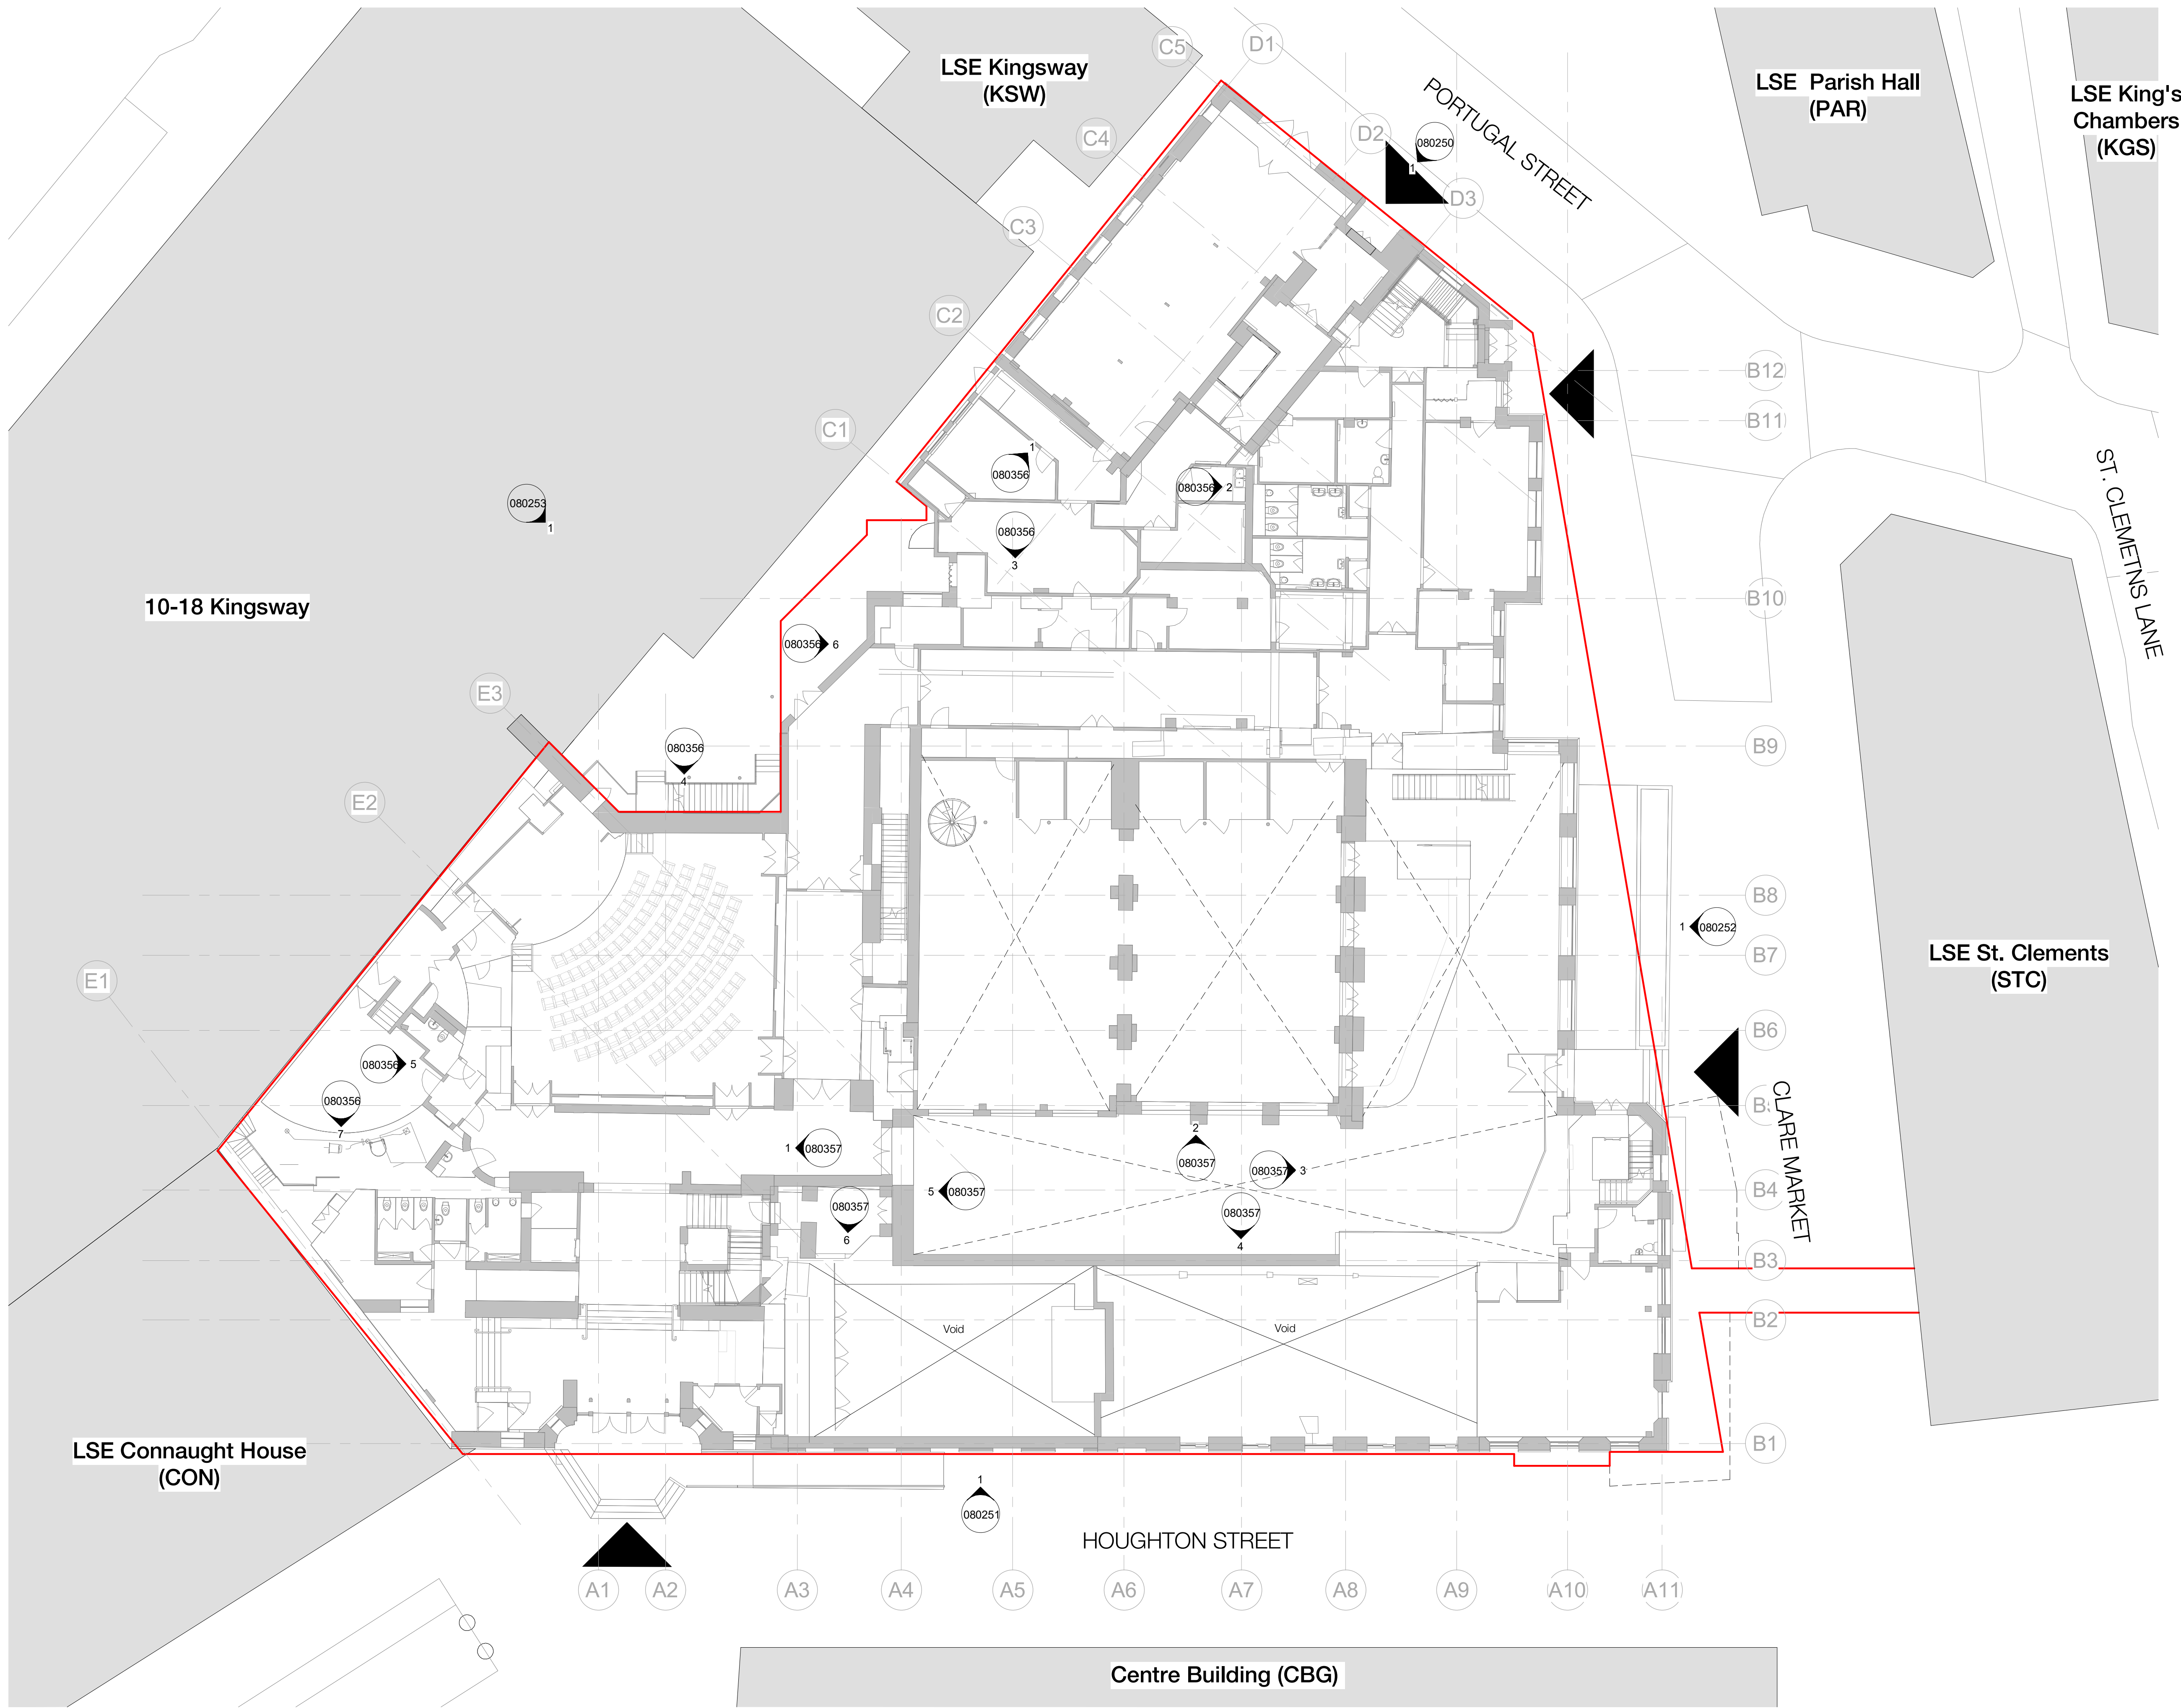

Ground Floor Plan - Proposed
1 : 150

Copyright Hawkins\Brown Architects
No implied licence exists. This drawing should not be used to calculate areas for the purposes of valuation. Do not scale this drawing. All dimensions to be checked on the site by the contractor and such dimensions to be their responsibility. All work must comply with relevant British Standards and Building Regulations requirements. Drawing errors and omissions to be reported to the architect. To be read in conjunction with Architect's specification and other consultant information.

Rev	Description	Date
P1	Planning	07.12.22

Wall Key

- Existing Wall
- Proposed Wall
- Site Boundary

159 St John Street
London EC1V 4QU

mail@hawkinsbrown.com
hawkinsbrown.com

Hawkins\Brown

Project
LSE Old Building Refurbishment
Houghton St
London WC2A 2AE
UK

Drawing
Proposed Plan Level 00

Scale @ A1
1 : 150

Date
07/12/22

Drawn By
CG

Checked By
RG

Job Number
210224

Status
S2

Purpose of Issue
For Approval

Drawing No.
LSEOLD-HBA-V1-00-DR-A-080150 P1

Rev