


Existing black metal soffit cladding
and all light fittings to be removed

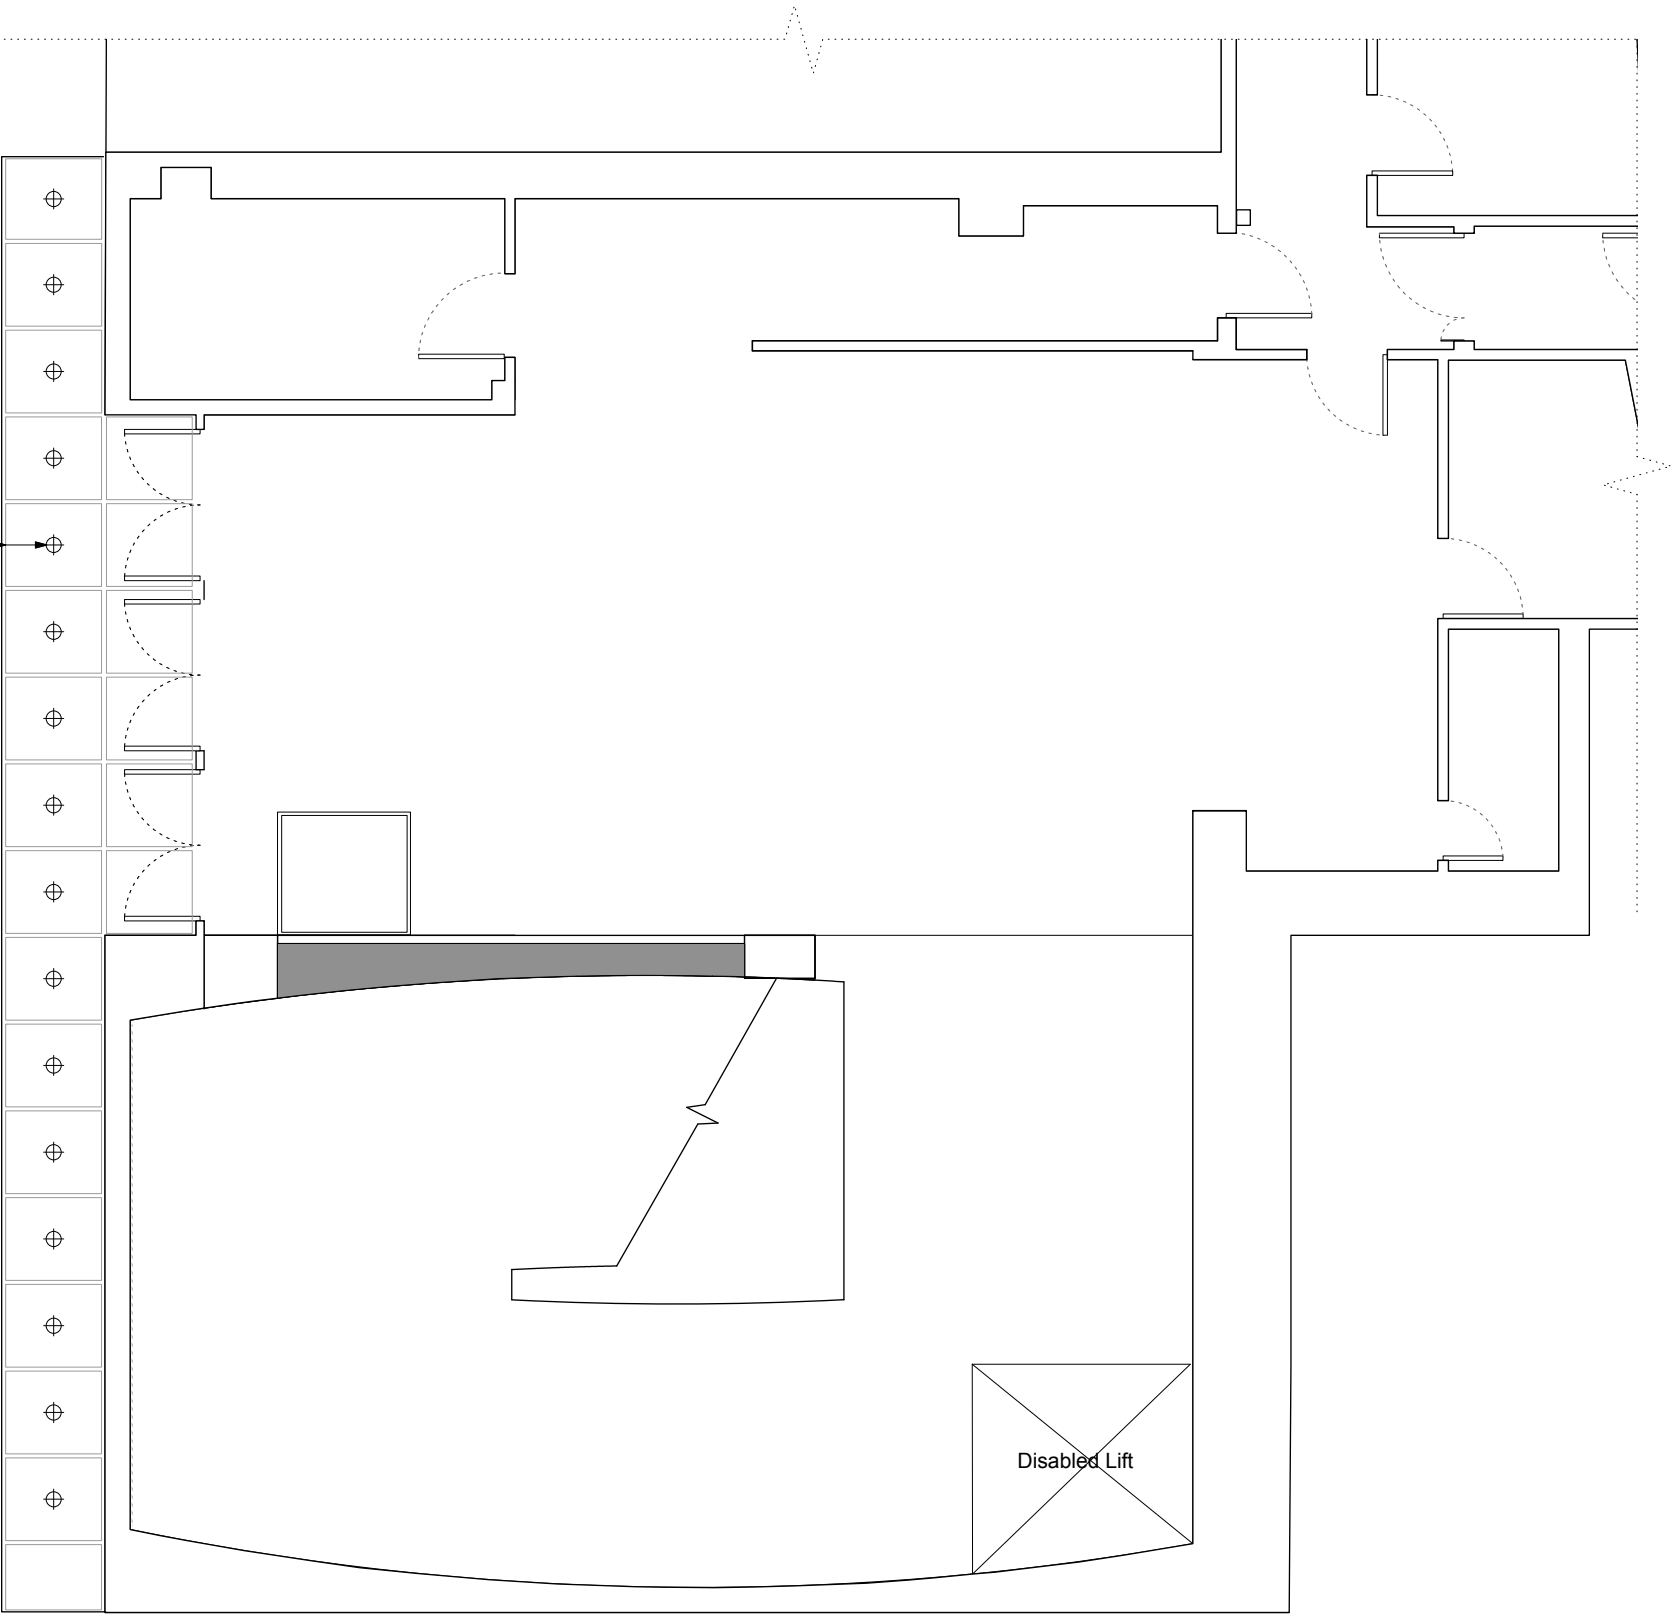

1 Level 00 Existing RCP
1:75

0 .5 1 2



GENERAL NOTES.

All dimensions to be checked on site prior to commencement of any works, and/or preparation of any shop drawings.

Sizes of and dimensions to any structural elements are indicative only. See structural engineers drawings for actual sizes / dimensions.

Sizes of and dimensions to any service elements are indicative only. See service engineers drawings for actual sizes and dimensions.

This drawing to be read in conjunction with all other Architect's drawings, specifications and other Consultants' information.


All proprietary systems shown on this drawing are to be installed strictly in accordance with the Manufacturers/Suppliers recommended details.

Any discrepancies between information shown on this drawing and any other contract information or manufacturers/suppliers recommendations is to be brought to the attention of the Architect

DO NOT SCALE FROM THIS DRAWING.

NOTES.

ALL DIMENSIONS TO BE CONFIRMED ON SITE!

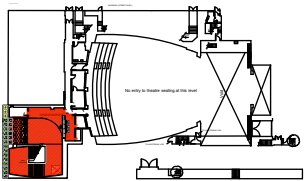

P1 Planning 22.08.14

REVISION DATE

Feix&Merlin Architects
Unit 40 | South City Court
52 Peckham Grove | London SE15 6FR
www.feixandmerlin.com

CLIENT London School of Economics
Saddler's Wells

PROJECT PEACOCK THEATRE
Refurbishment

DRAWING **REFLECTIVE CEILING PLAN**
Ground Floor EXISTING

SCALE 1:75@ A3 (NTS@ A1)

DATE JUNE 2014 DRAWN BY F&M

DWG No. **0217 RC 00-1** REVISION P1

DRAWING STATUS **PLANNING**