


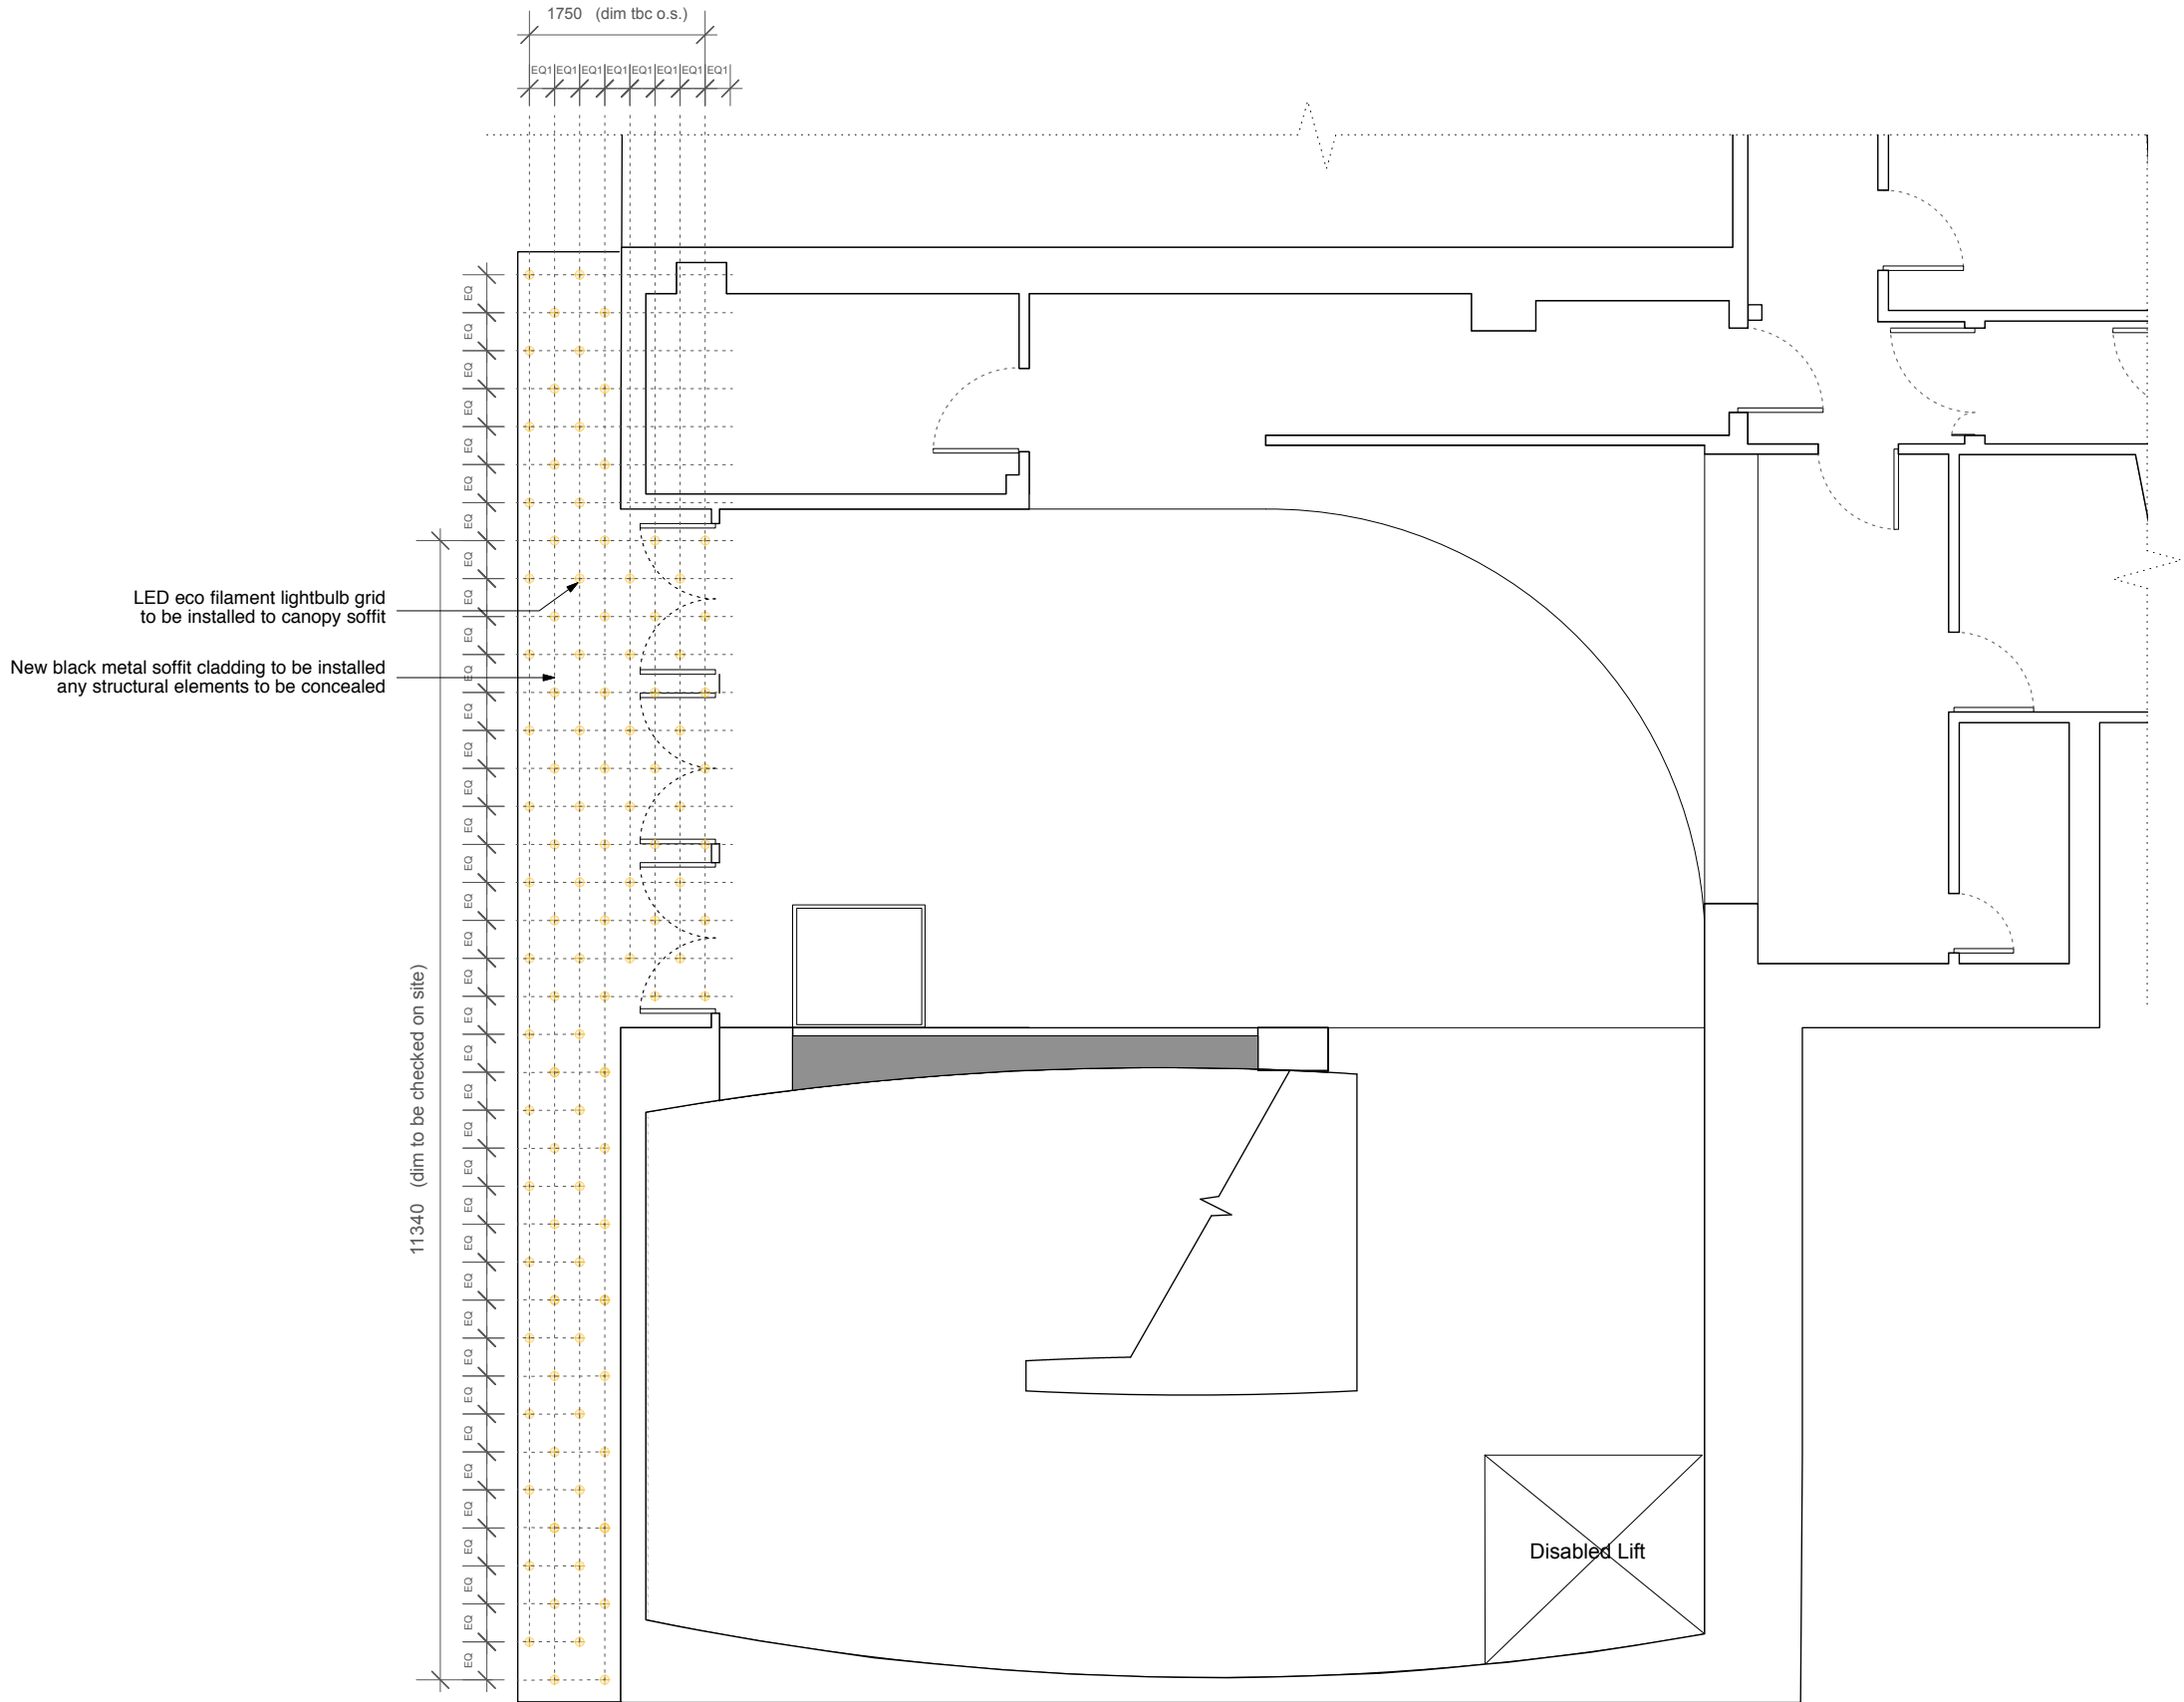

GENERAL NOTES.

All dimensions to be checked on site prior to commencement of any works, and/or preparation of any shop drawings.

Sizes of and dimensions to any structural elements are indicative only. See structural engineers drawings for actual sizes / dimensions.

Sizes of and dimensions to any service elements are indicative only. See service engineers drawings for actual sizes and dimensions.

This drawing to be read in conjunction with all other Architect's drawings, specifications and other Consultants' information.


All proprietary systems shown on this drawing are to be installed strictly in accordance with the Manufacturers/Suppliers recommended details.

Any discrepancies between information shown on this drawing and any other contract information or manufacturers/suppliers recommendations is to be brought to the attention of the Architect

DO NOT SCALE FROM THIS DRAWING.

NOTES.

ALL DIMENSIONS TO BE CONFIRMED ON SITE!

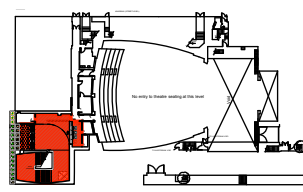

LED eco filament lightbulb to be installed in grid

1 Level 00 Proposed RCP
1:75



P1	Planning	22.08.14
REVISION		DATE
Feix&Merlin Architects Unit 40 South City Court 52 Peckham Grove London SE15 6FR www.feixandmerlin.com		
CLIENT	London School of Economics Saddler's Wells	
PROJECT	PEACOCK THEATRE Refurbishment	
DRAWING	REFLECTIVE CEILING PLAN Ground Floor PROPOSED	
SCALE	1:75@ A3 (NTS@ A1)	
DATE	JUNE 2014	DRAWN BY F&M
DWG No.	0217 RC 00-2	REVISION P1
DRAWING STATUS PLANNING		