


05


A

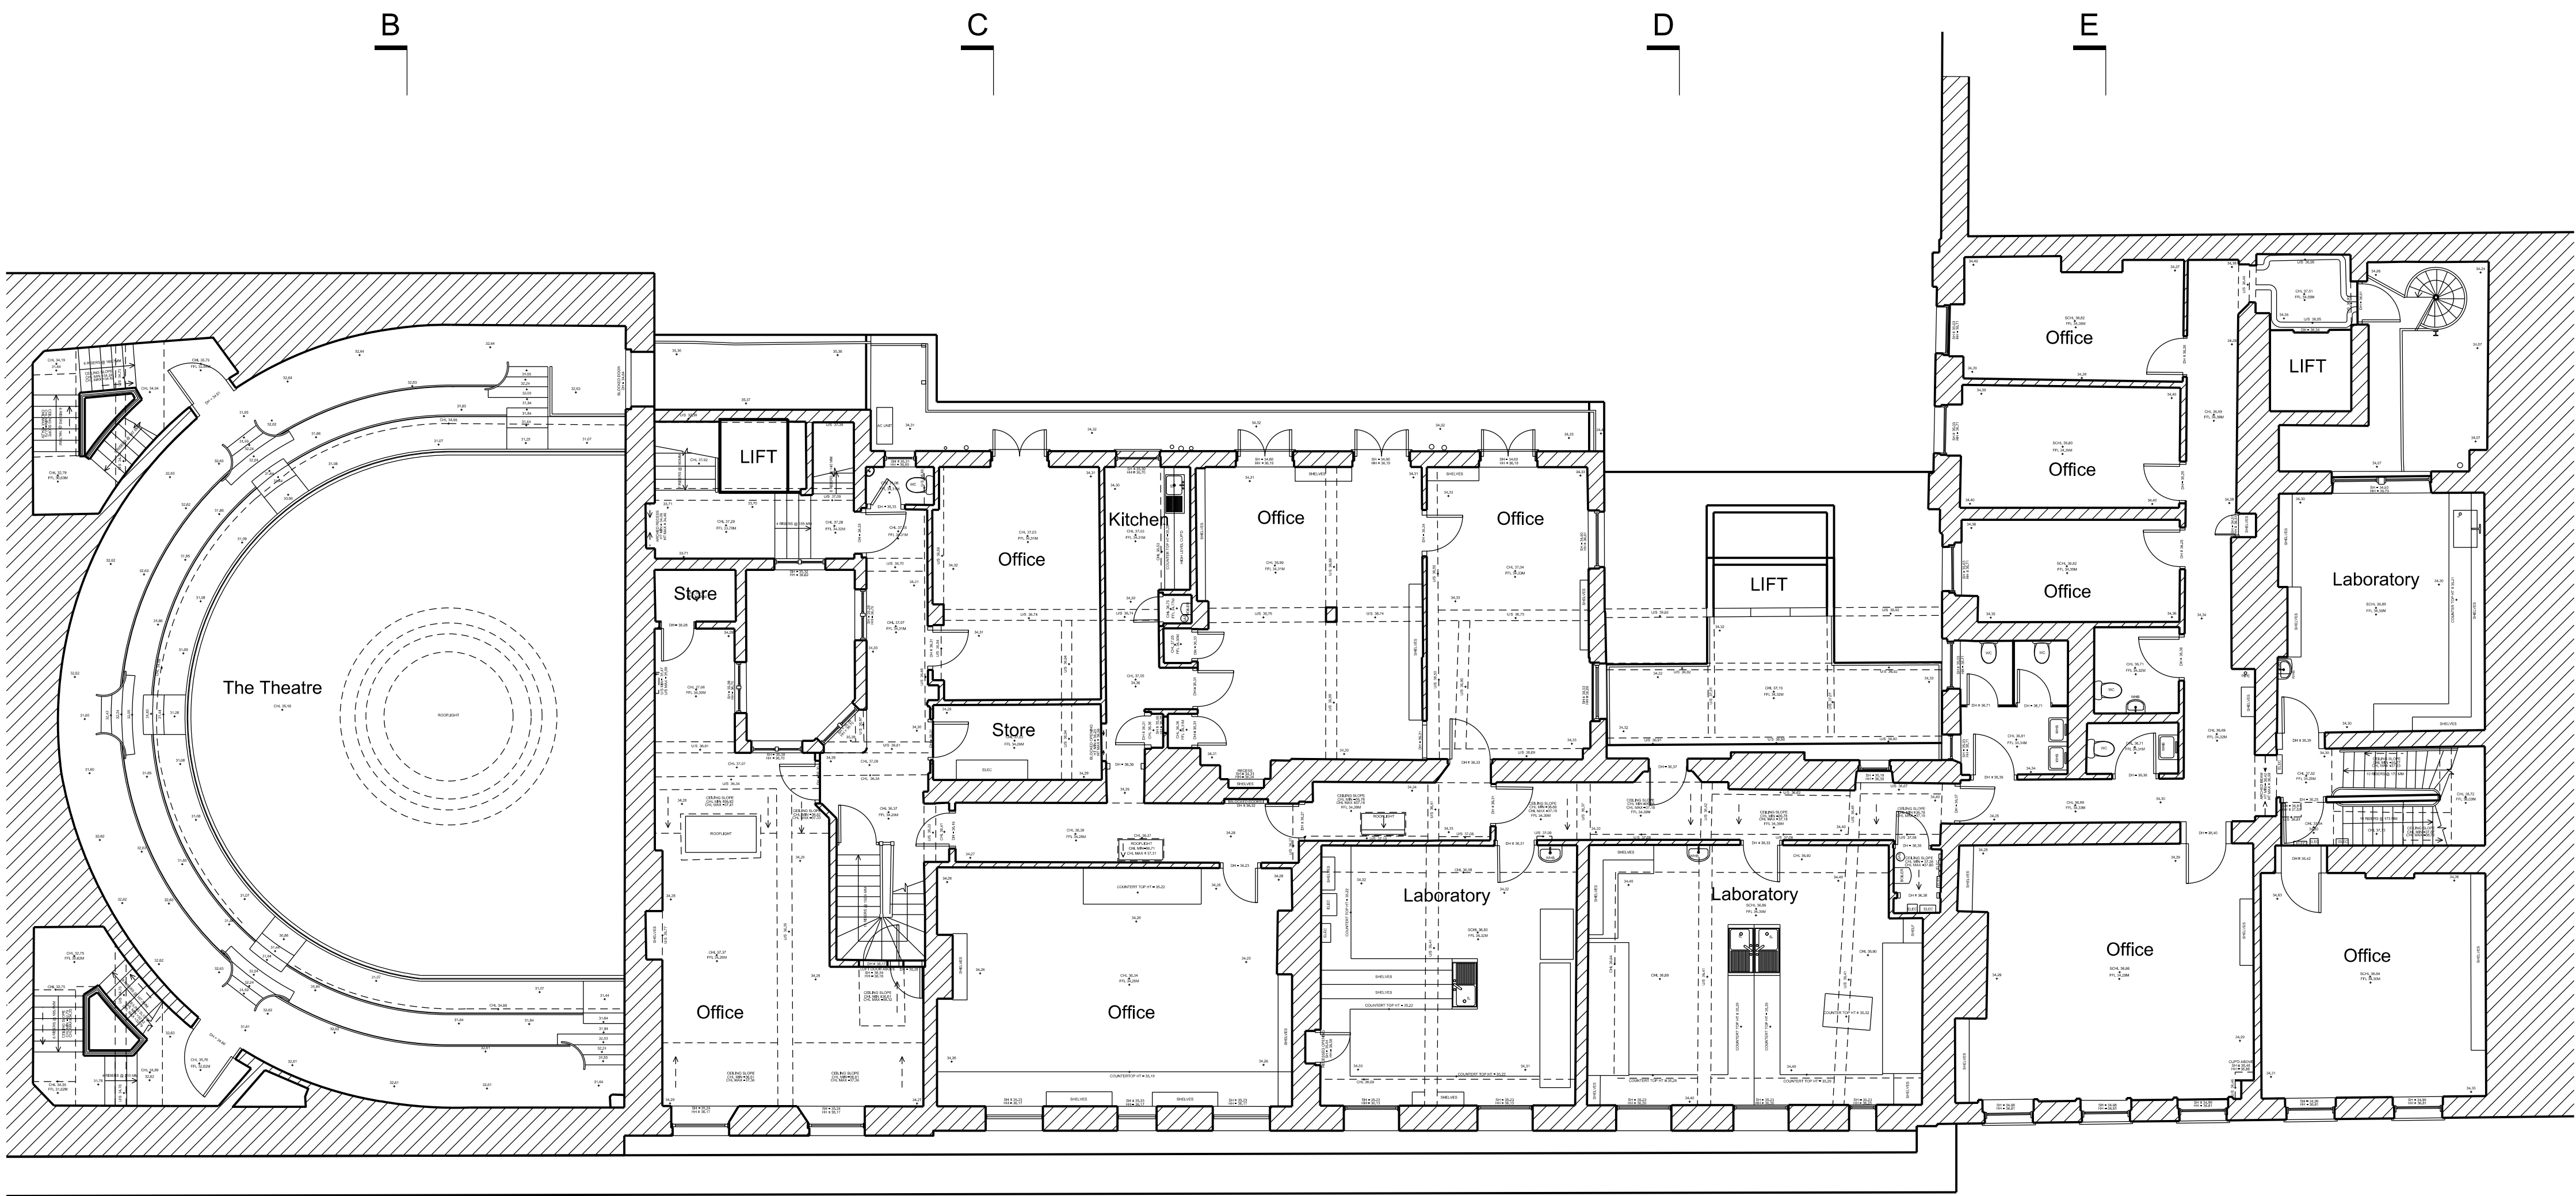

ALBEMARLE STREET

No.21 No.20

B C D E

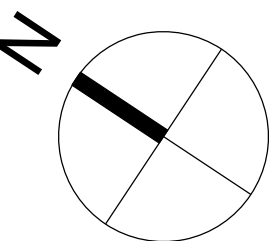

SCALE 1 : 100 0m 5m 10m

EXISTING THIRD FLOOR PLAN
1:100

equipment refer to HH
information

BUILDING DESIGN PARTNERSHIP LTD SHALL HAVE NO RESPONSIBILITY FOR ANY
USE MADE OF THIS DOCUMENT OTHER THAN FOR THAT WHICH IT WAS PREPARED
AND ISSUED.
ALL DIMENSIONS SHOULD BE CHECKED ON SITE.
DO NOT SCALE FROM THIS DRAWING.
ANY DRAWING ERRORS OR DISCREPANCIES SHOULD BE BROUGHT TO THE
ATTENTION OF BUILDING DESIGN PARTNERSHIP LTD AT THE ADDRESS SHOWN
BELOW

NOTES

NOTE: All site dimensions require final
site survey.

Based on measured survey
SOVA240415 MBS by Sovia.

Drawing to be read in conjunction
with all associated BDP Significance
Plans, specification and information,
and Harley Haddow (BSE) and Price &
Myers (C+S) information.


Key:

S Stair
L Lift

W.01 Window Code
XXX

D.01 Door Code
XXX

P01: PLANNING & LBC	LB	DA 28.02.25
DESIGN REVISION	DATE	BY

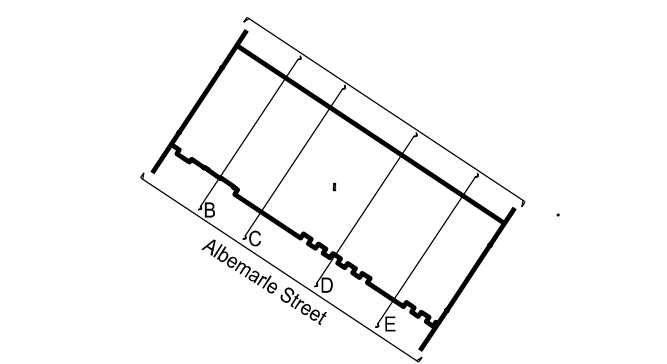

THE ROYAL INSTITUTION
21 Albemarle Street
London,
W1S 4BS

Ri The Royal Institution
Science Lives Here

BDP.
16 Brewhouse Yard
Clerkenwell
London, EC1V 4LJ
United Kingdom
T +44 (0)20 7812 8000
F +44 (0)20 7812 8399
www.bdp.com

PROJECT TITLE	THE ROYAL INSTITUTION FOOTPRINT PROJECT
PROJECT NO.	P3003732
DOCUMENT TITLE	EXISTING THIRD FLOOR PLAN
SCALE	1:100@A0
DATE	28.02.2025
DESIGNER	00ap003
ISSUED	P01