


05

A |

| A

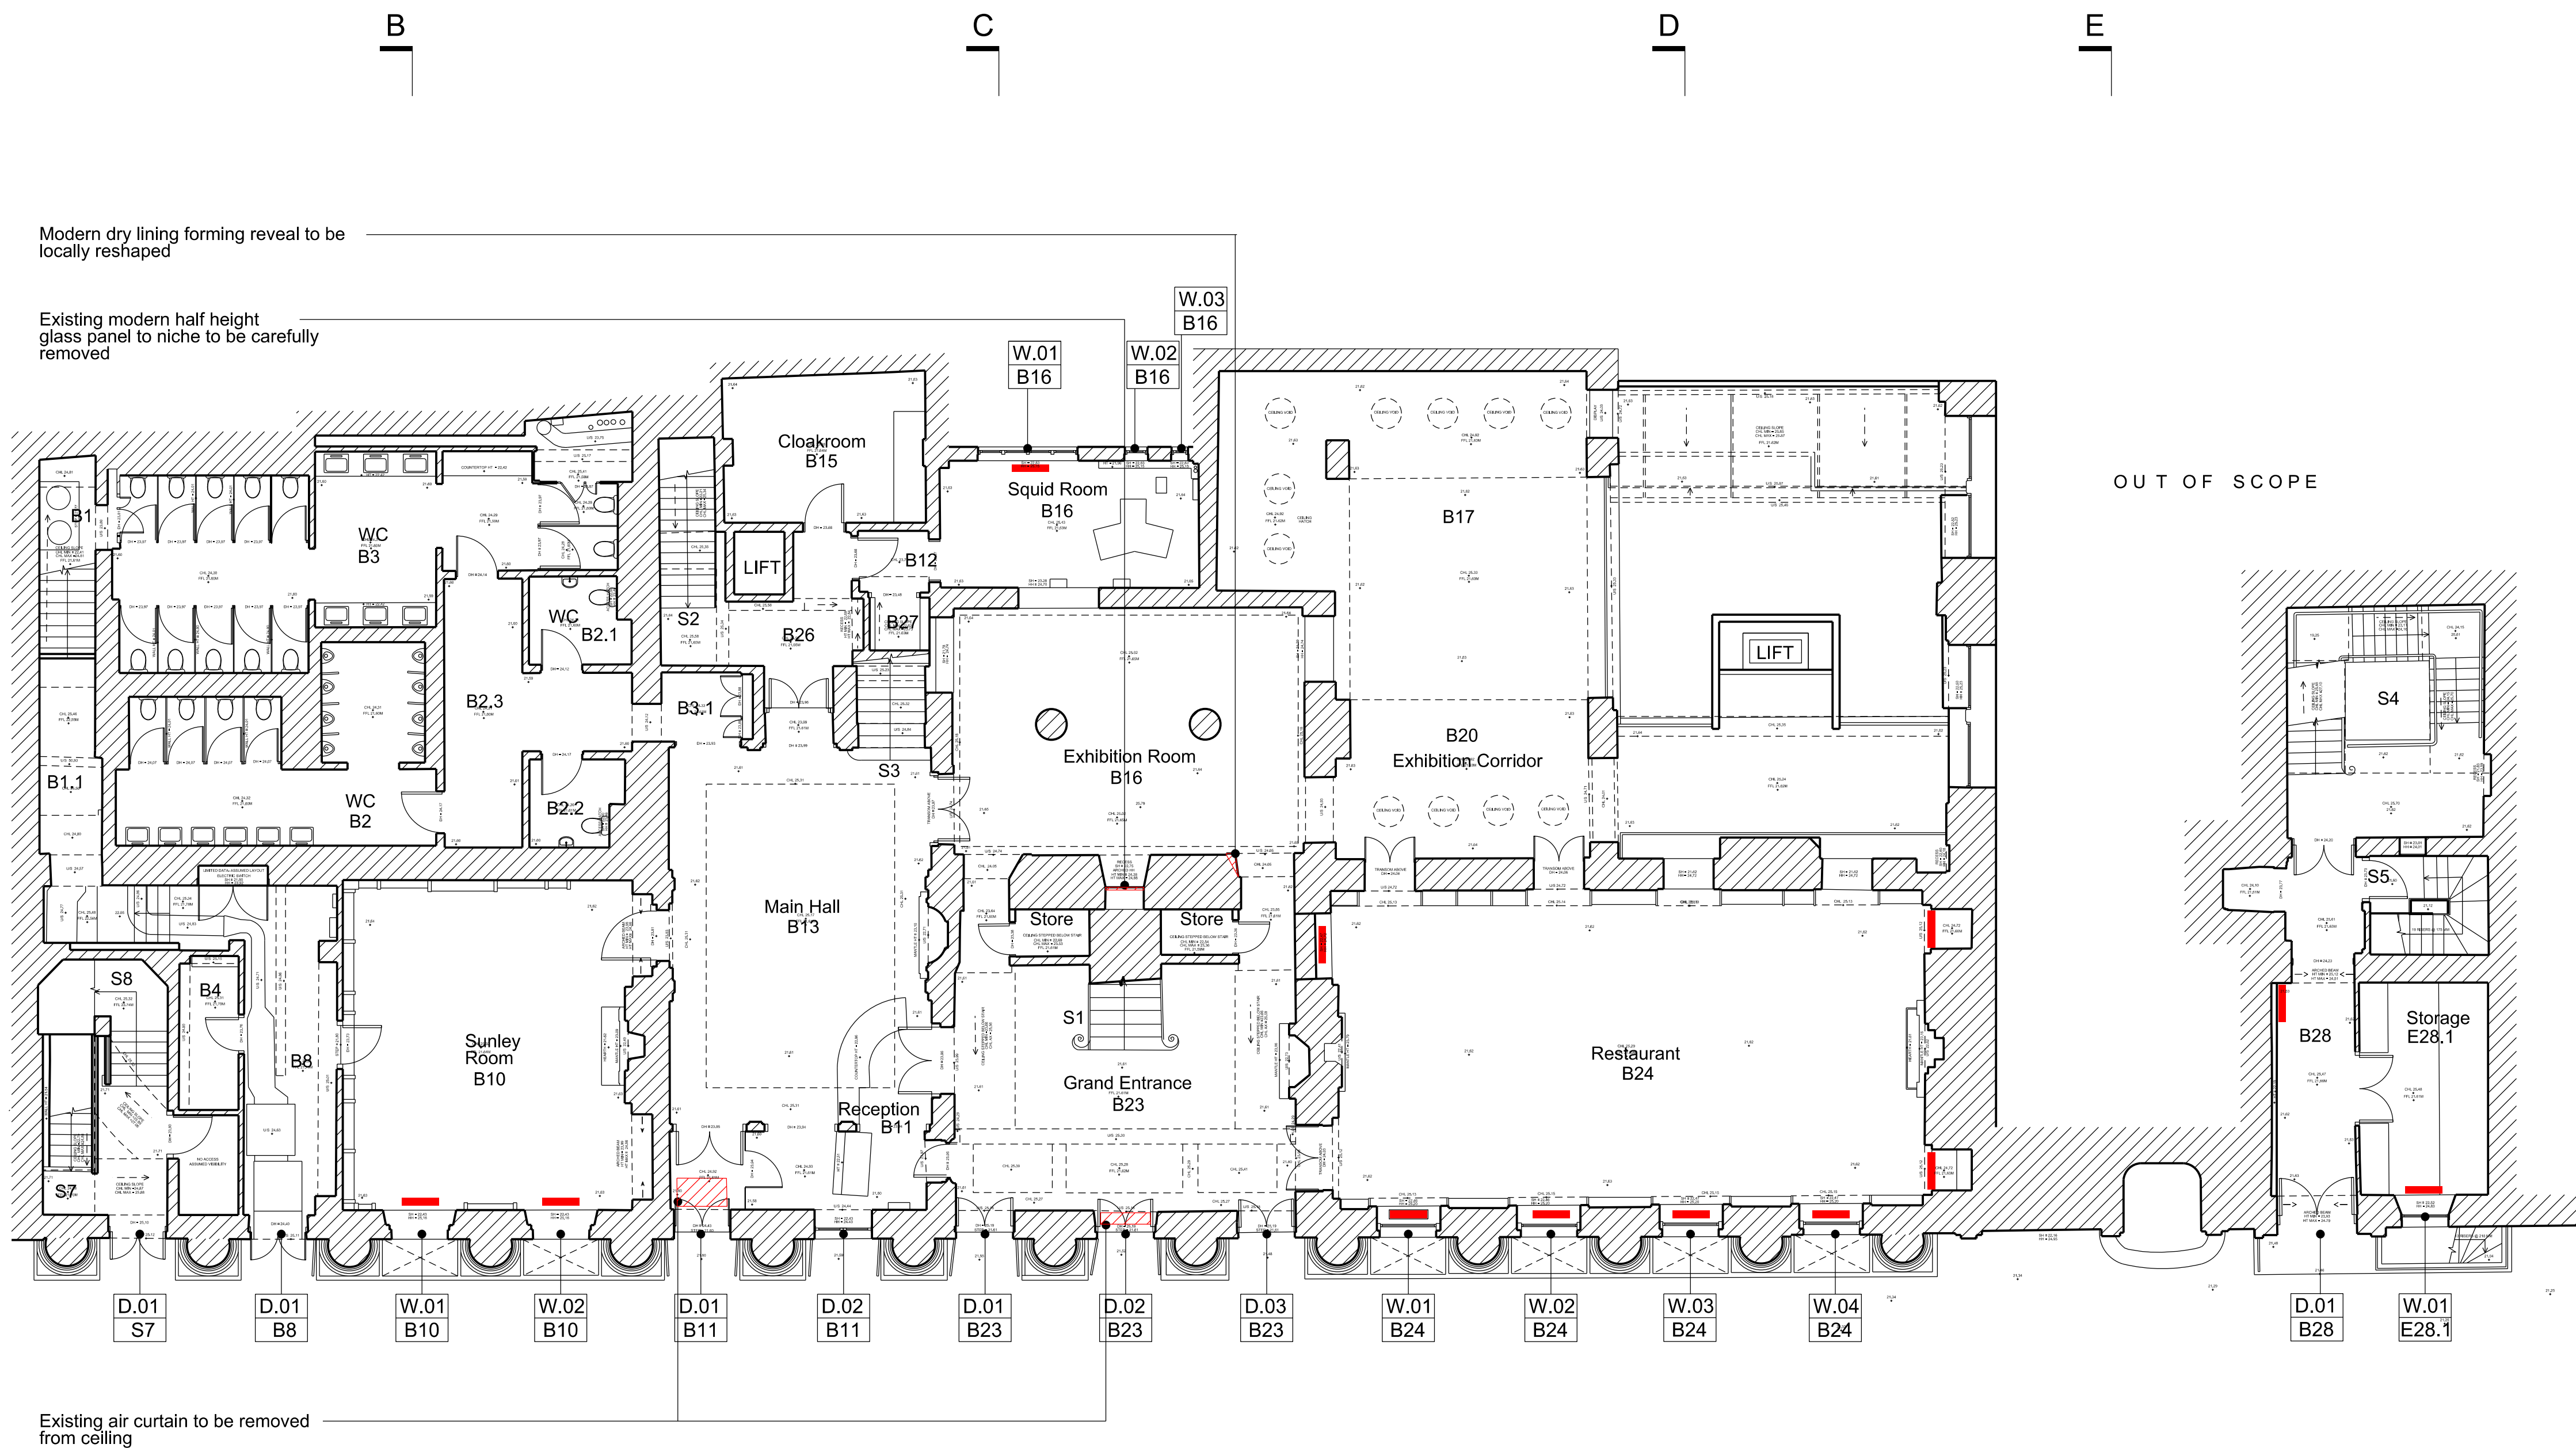

PROPOSED GROUND FLOOR PLAN - Fabric Removals
1:100

KEY

Existing non-heritage/significant radiators and heat emitters to be carefully removed

Proposed removals

For removal of all existing plant and heating and cooling equipment refer to HH information

BUILDING DESIGN PARTNERSHIP LTD SHALL HAVE NO RESPONSIBILITY FOR ANY USE MADE OF THIS DOCUMENT OTHER THAN THAT WHICH IT WAS PREPARED AND ISSUED.

ALL DIMENSIONS SHOULD BE CHECKED ON SITE. DO NOT SCALE FROM THIS DRAWING.

ANY DRAWING ERRORS OR DISCREPANCIES SHOULD BE BROUGHT TO THE ATTENTION OF BUILDING DESIGN PARTNERSHIP LTD AT THE ADDRESS SHOWN BELOW.

NOTES

NOTE: All site dimensions require final site survey.

Based on measured survey SOVA240415 MBS by Sovia.

Drawing to be read in conjunction with all associated BDP Significance Plans, specification and information, and Harley Haddow (BSE) and Price & Myers (C+S) information.

Key:

S Stair
L Lift

W.01 Window Code
XXX

D.01 Door Code
XXX

P01: PLANNING & LBC		LB	DA	28.02.25
DATE		DATE	DATE	DATE
28.02.25		28.02.25	28.02.25	28.02.25

21 Albemarle Street

The Royal Institution
21 Albemarle Street
London,
W1S 4BS

Ri The Royal Institution
Science Lives Here

BDP.

16 Brewhouse Yard
Clerkenwell
London, EC1V 4LJ
United Kingdom

T +44 (0)20 7812 8000
F +44 (0)20 7812 8399
www.bdp.com

PROJECT
THE ROYAL INSTITUTION
FOOTPRINT PROJECT

P3003732

PROPOSED GROUND FLOOR PLAN
FABRIC REMOVALS

SCALE
1:100@A0

DATE
28.02.2025

PROJECT
18ap00G

PROJECT
P01