


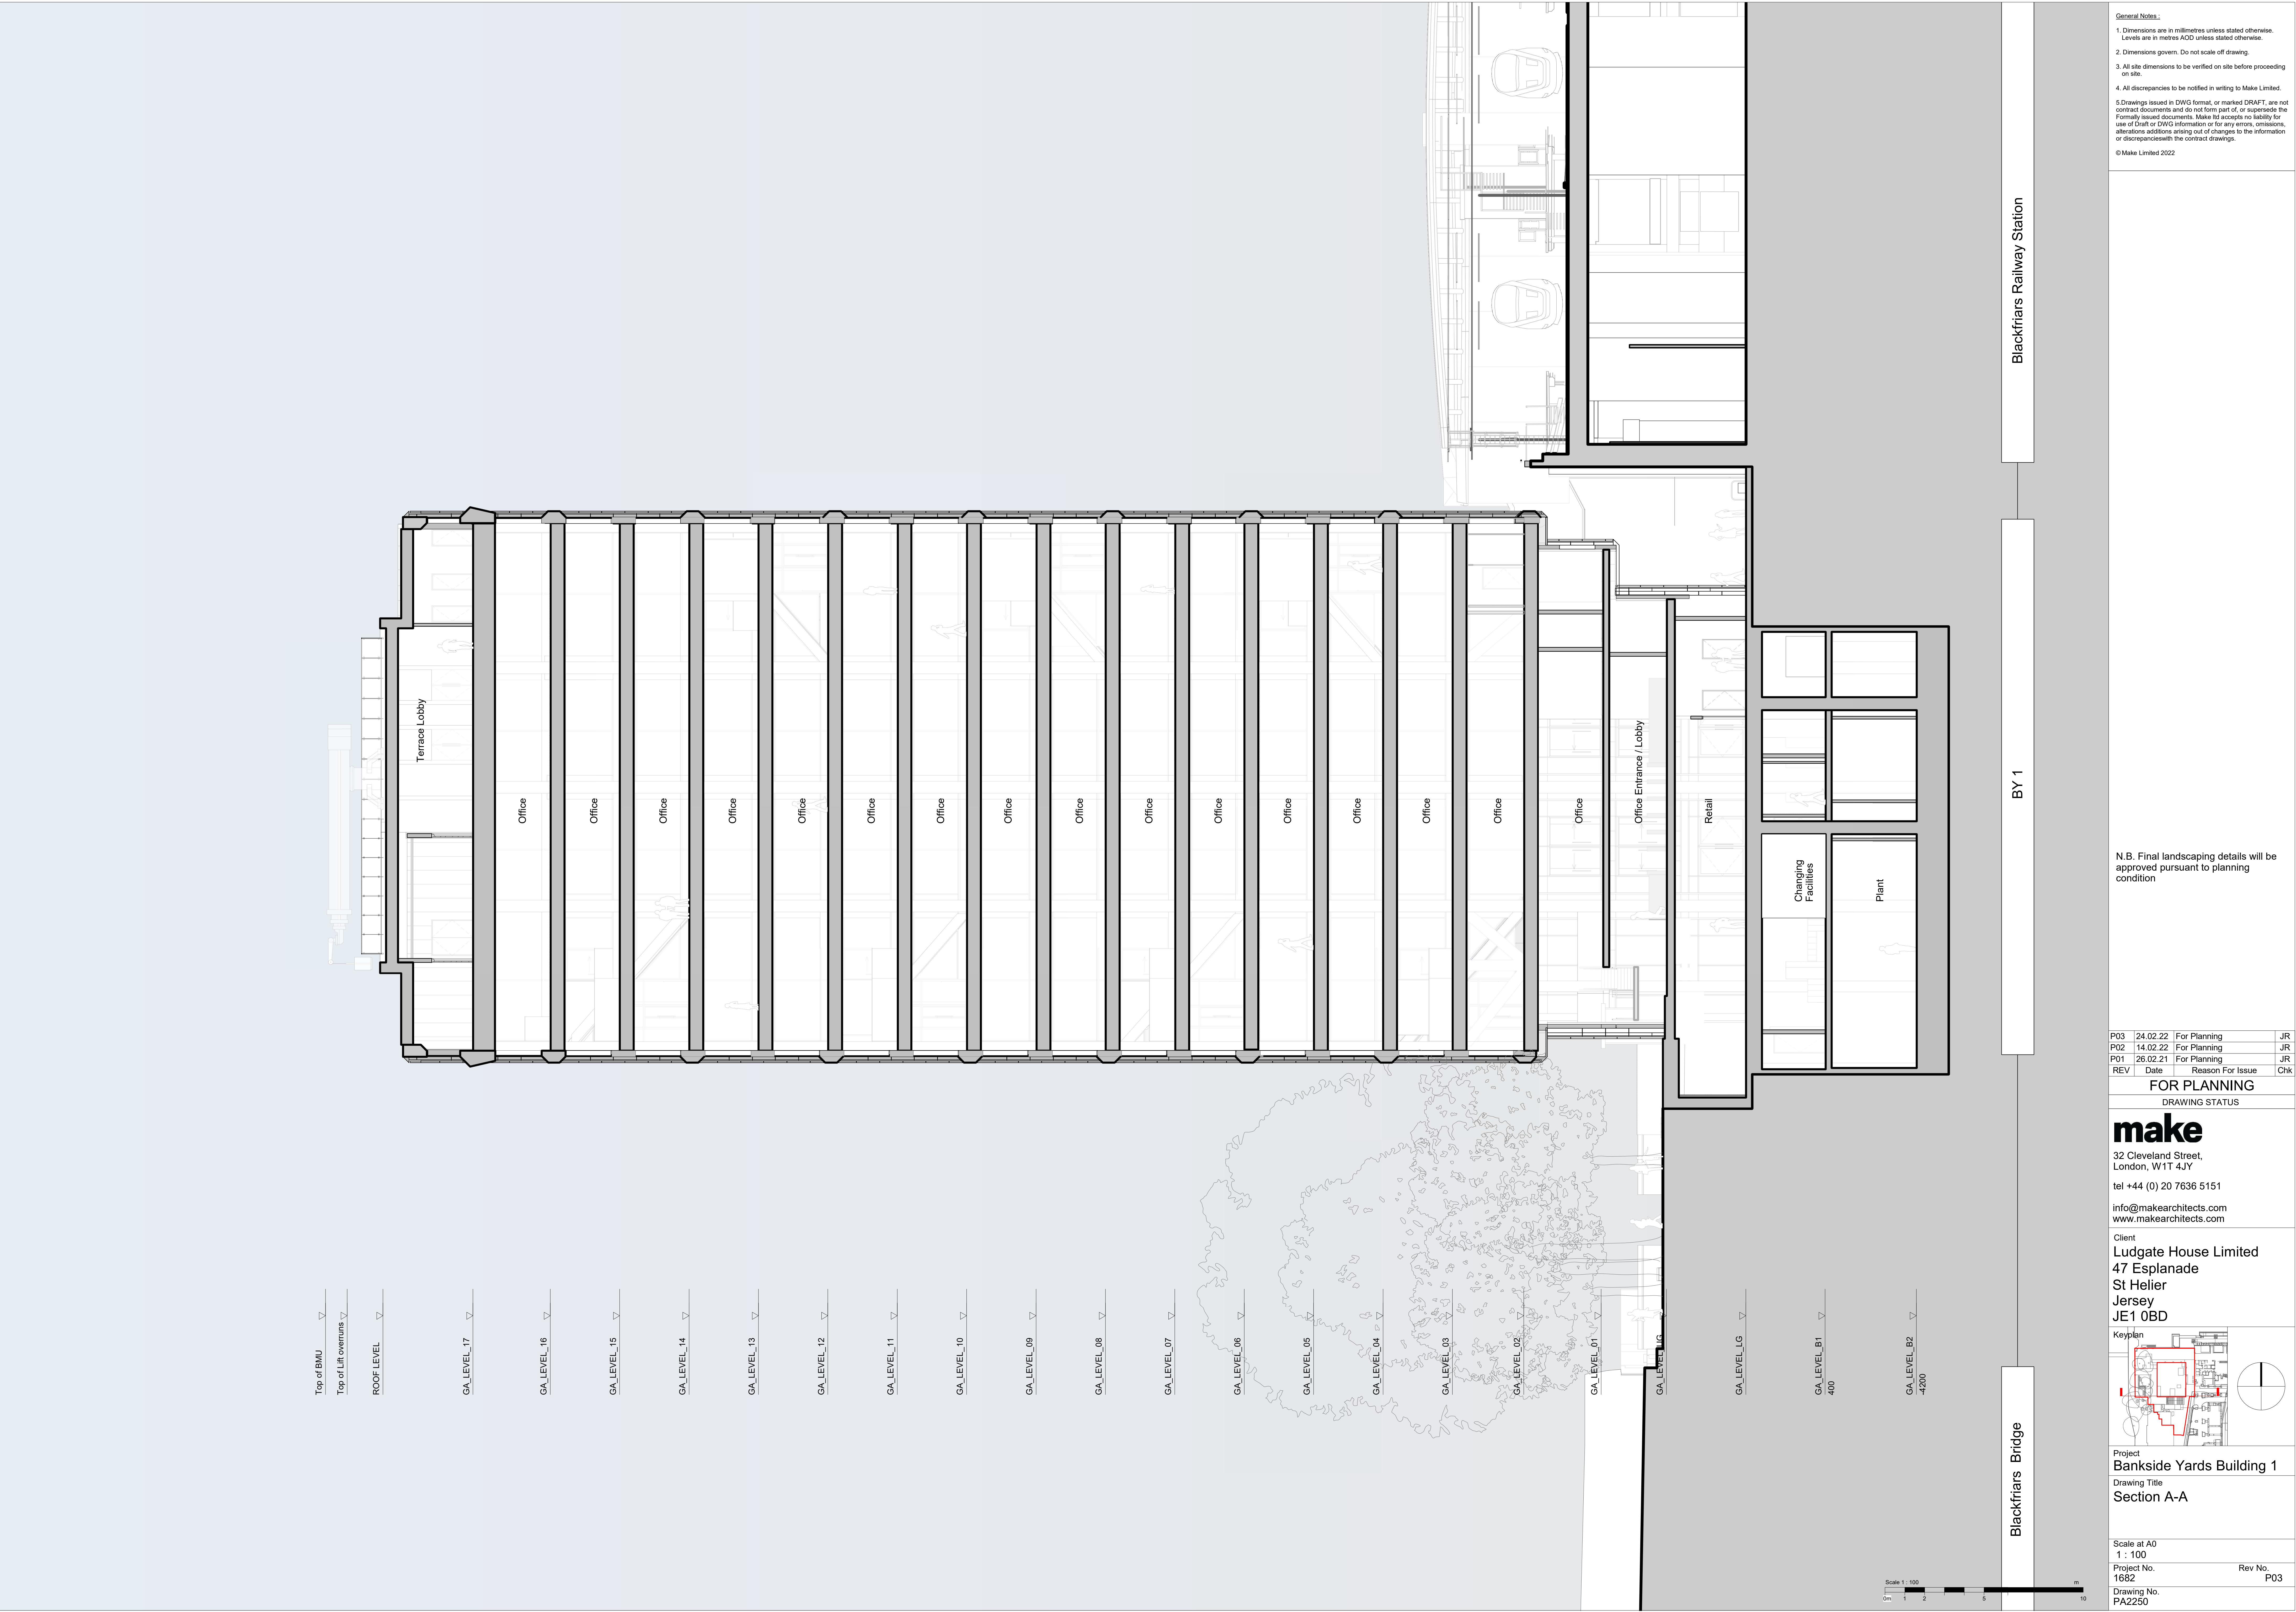

General Notes:

1. Dimensions are in millimetres unless stated otherwise.
Levels are in metres AOD unless stated otherwise.
2. Dimensions govern. Do not scale off drawing.
3. All site dimensions to be verified on site before proceeding on site.
4. All discrepancies to be notified in writing to Make Limited.
5. Drawings issued in DWG format, or marked DRAFT, are not contract documents and do not form part of, or supersede the contract documents. Make Ltd accepts no liability for use of Draft or DWG information or for any errors, omissions, alterations additions arising out of changes to the information or discrepancies with the contract drawings.

© Make Limited 2022


N.B. Final landscaping details will be approved pursuant to planning condition

P03	24.02.22	For Planning	JR
P02	14.02.22	For Planning	JR
P01	26.02.21	For Planning	JR
REV	Date	Reason For Issue	Chk

FOR PLANNING
DRAWING STATUS

make
32 Cleveland Street,
London, W1T 4JY
tel +44 (0) 20 7636 5151
info@makearchitects.com
www.makearchitects.com

Client
Ludgate House Limited
47 Esplanade
St Helier
Jersey
JE1 0BD

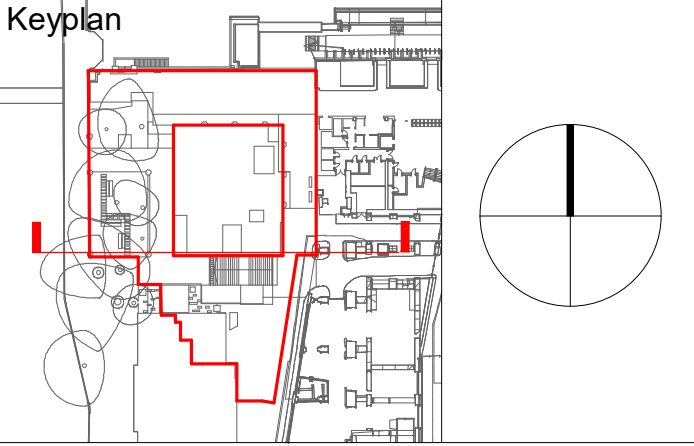

Project
Bankside Yards Building 1
Drawing Title
Section A-A

Scale at A0
1 : 100
Project No.
1682
Drawing No.
PA2250

Rev No.
P03