


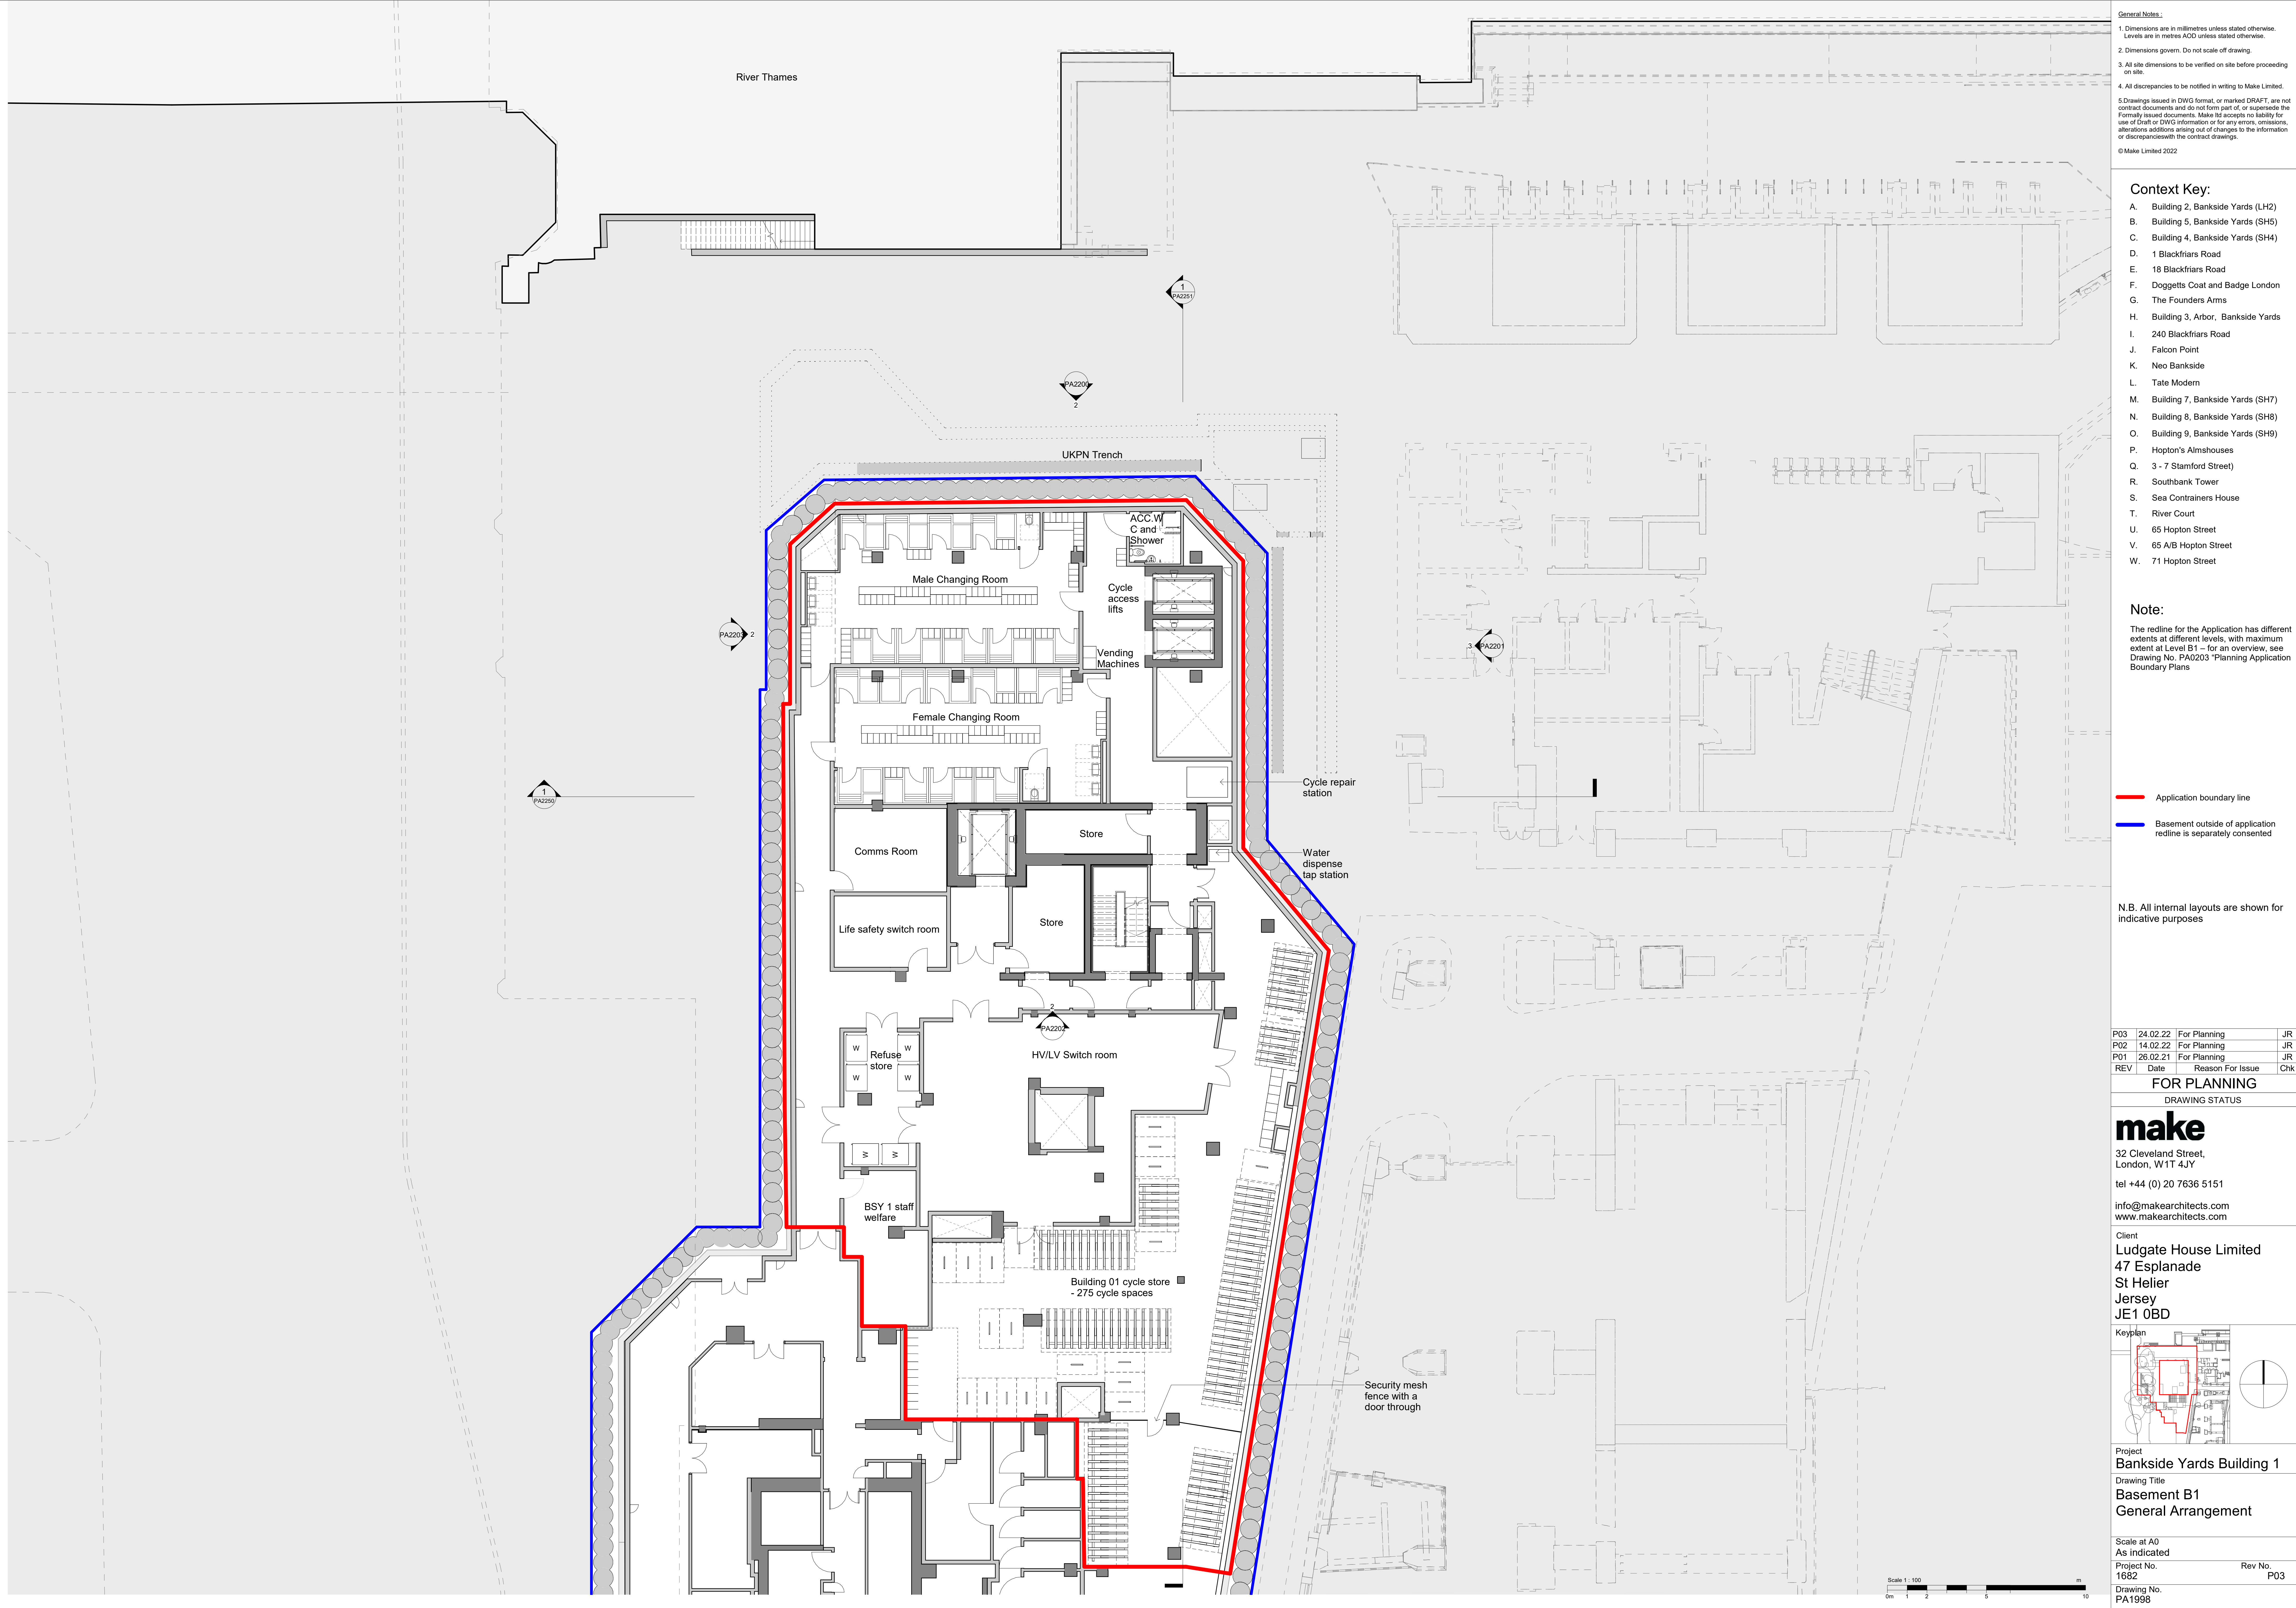

General Notes:

1. Dimensions are in millimetres unless stated otherwise. Levels are in metres AOD unless stated otherwise.
2. Dimensions govern. Do not scale off drawing.
3. All site dimensions to be verified on site before proceeding on site.
4. All discrepancies to be notified in writing to Make Limited.
5. Drawings issued in DWG format, or marked DRAFT, are not contract documents and do not form part of, or supersede the. Formally issued documents. Make Ltd accepts no liability for use of Draft or DWG information or for any errors, omissions, alterations additions arising out of changes to the information or discrepancies with the contract drawings.

© Make Limited 2022

- Context Key:**
- A. Building 2, Bankside Yards (LH2)
 - B. Building 5, Bankside Yards (SH5)
 - C. Building 4, Bankside Yards (SH4)
 - D. 1 Blackfriars Road
 - E. 18 Blackfriars Road
 - F. Doggetts Coat and Badge London
 - G. The Founders Arms
 - H. Building 3, Arbor, Bankside Yards
 - I. 240 Blackfriars Road
 - J. Falcon Point
 - K. Neo Bankside
 - L. Tate Modern
 - M. Building 7, Bankside Yards (SH7)
 - N. Building 8, Bankside Yards (SH8)
 - O. Building 9, Bankside Yards (SH9)
 - P. Hopton's Almshouses
 - Q. 3 - 7 Stamford Street
 - R. Southbank Tower
 - S. Sea Containers House
 - T. River Court
 - U. 65 Hopton Street
 - V. 65 A/B Hopton Street
 - W. 71 Hopton Street

Note:

The redline for the Application has different extents at different levels, with maximum extent at Level B1 – for an overview, see Drawing No. PA0203 'Planning Application Boundary Plans'

- Application boundary line
- Basement outside of application redline is separately consented

N.B. All internal layouts are shown for indicative purposes

P03	24.02.22	For Planning	JR
P02	14.02.22	For Planning	JR
P01	26.02.21	For Planning	JR
REV	Date	Reason For Issue	Chk

FOR PLANNING

DRAWING STATUS


make

32 Cleveland Street,
London, W1T 4JY

tel +44 (0) 20 7636 5151

info@makearchitects.com
www.makearchitects.com

Client
Ludgate House Limited
47 Esplanade
St Helier
Jersey
JE1 0BD

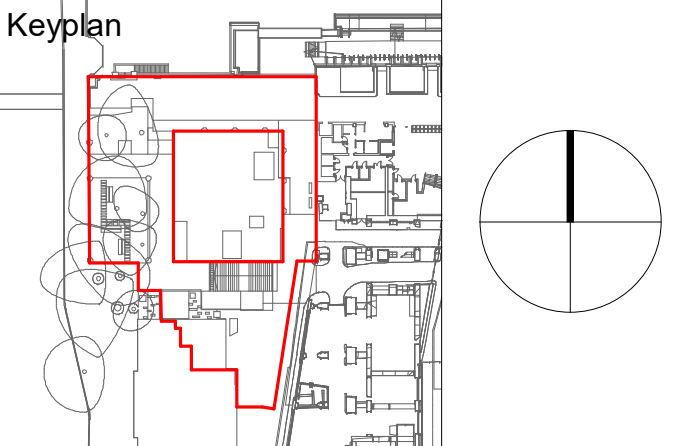

Project
Bankside Yards Building 1

Drawing Title
**Basement B1
General Arrangement**

Scale at A0
As indicated

Project No.
1662

Rev No.
P03

Drawing No.
PA1998