



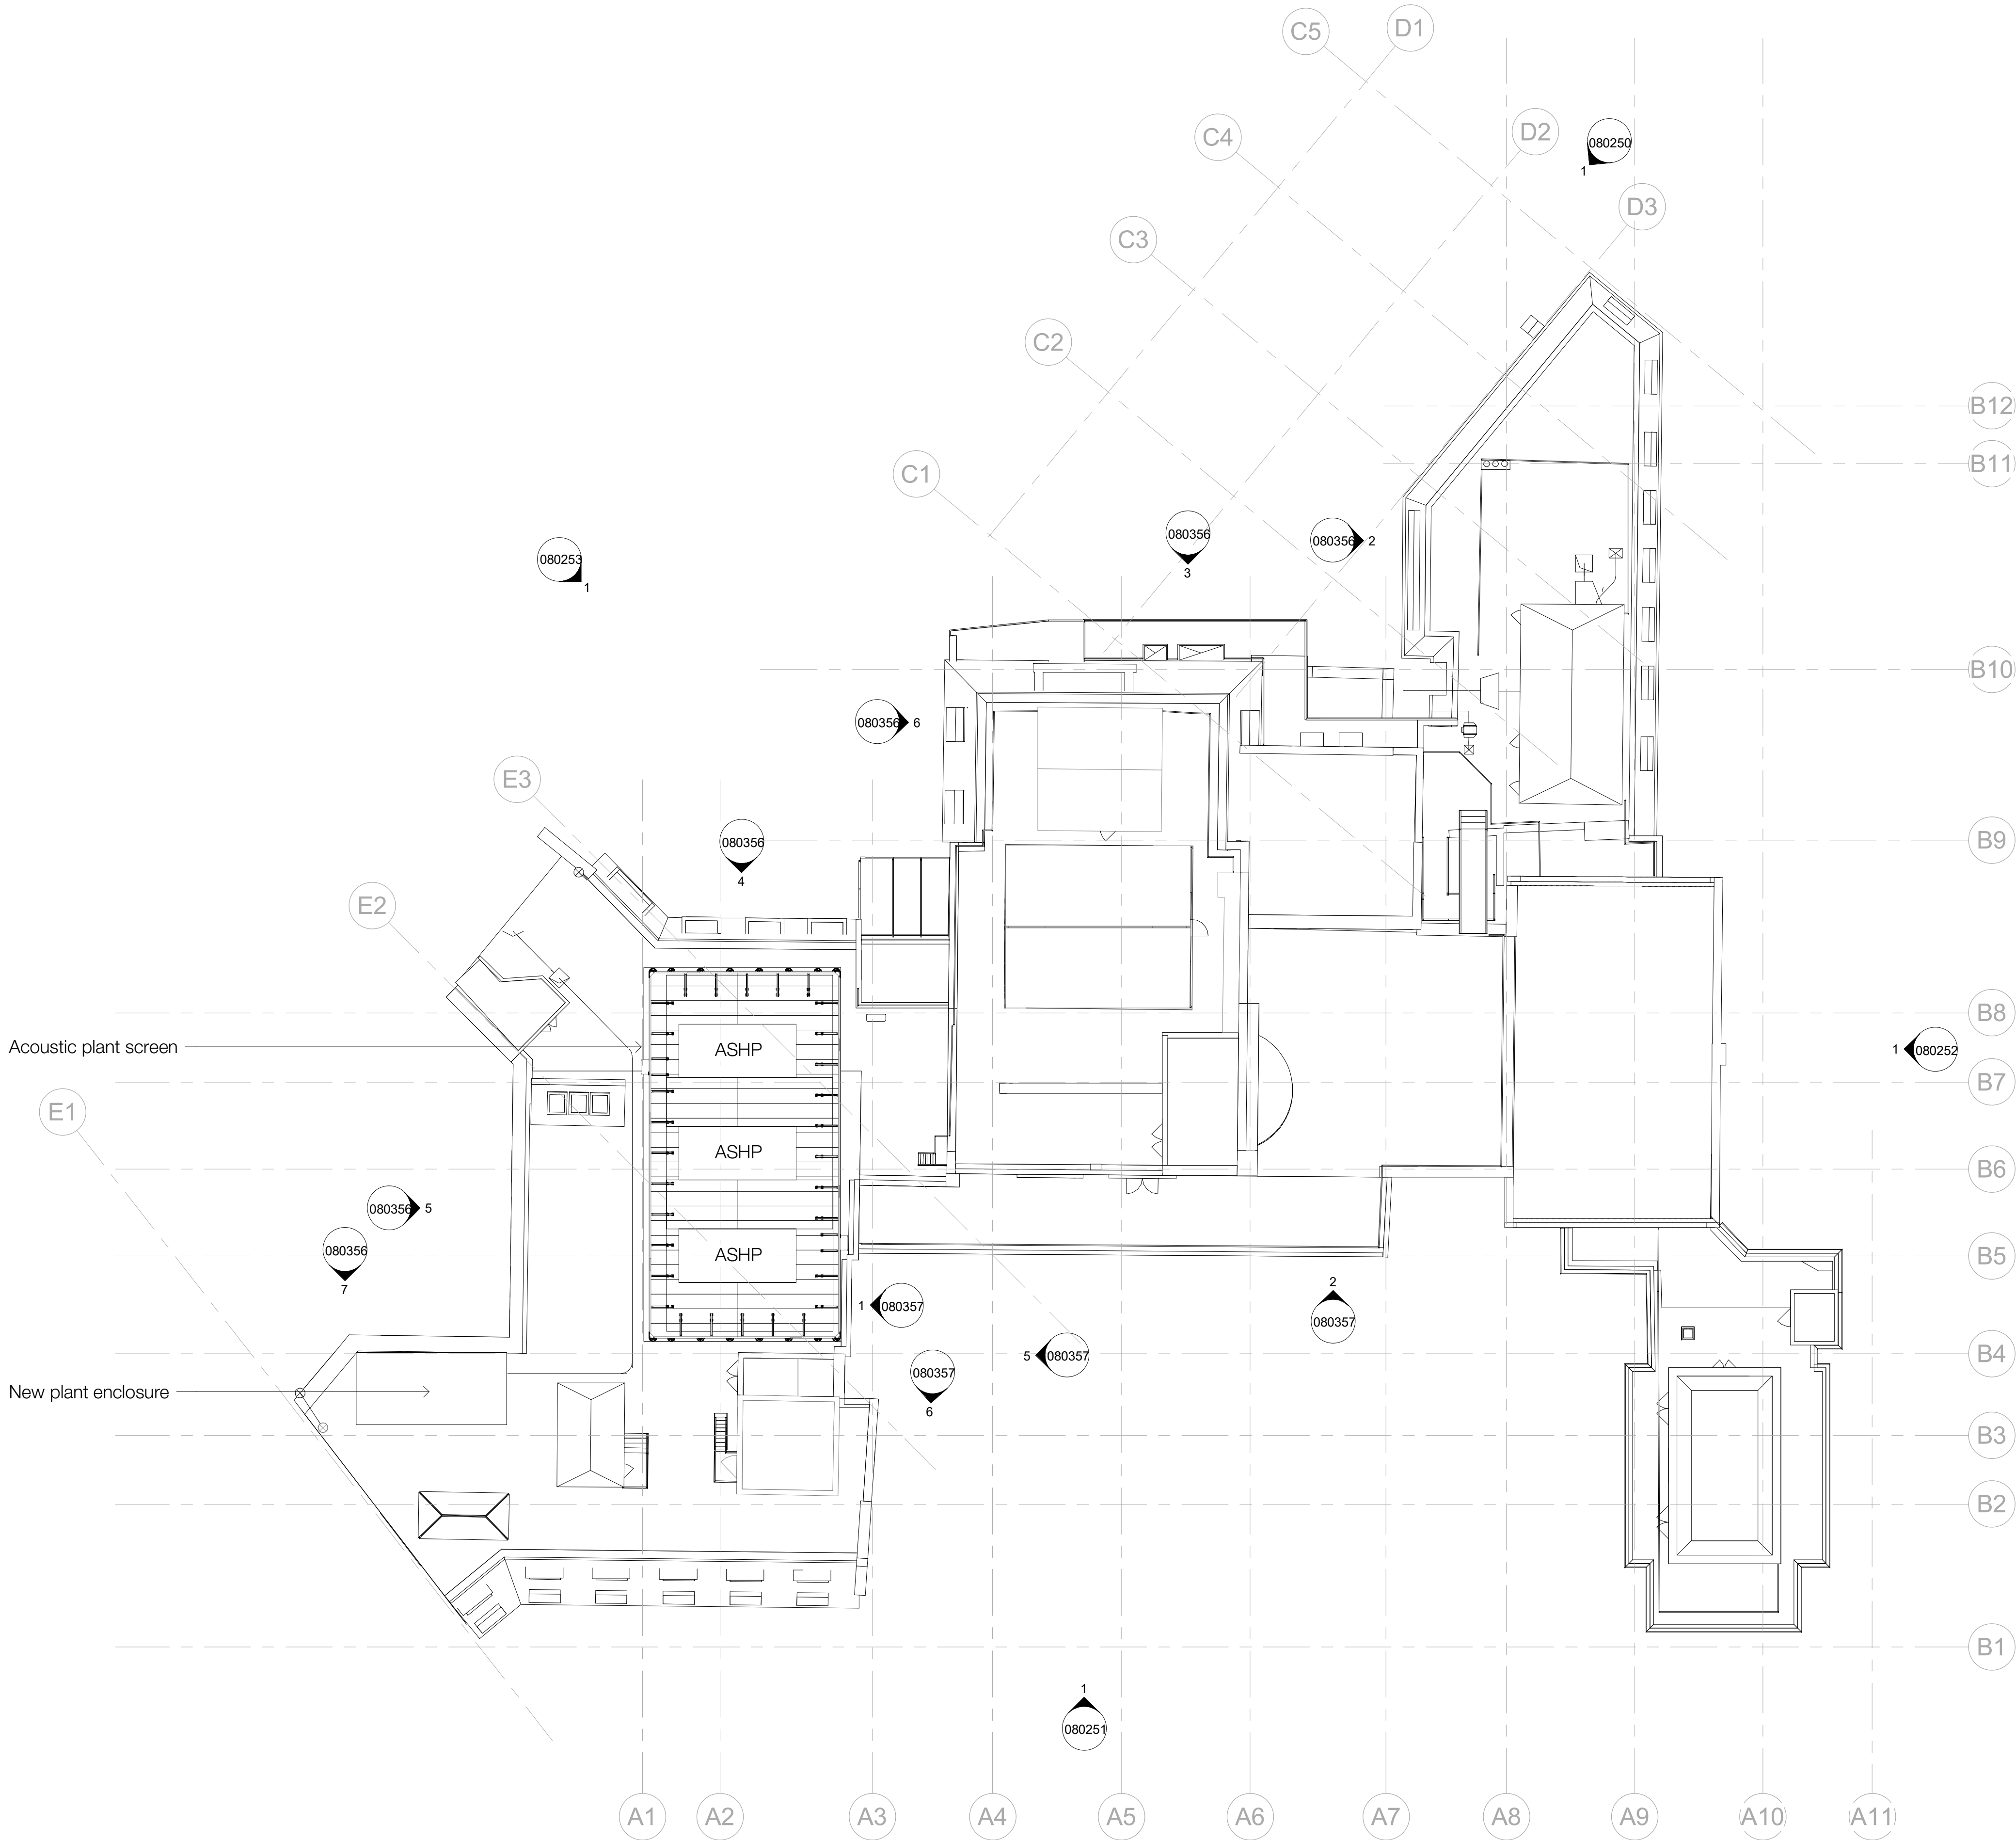

Roof Plan - Proposed
1 : 150

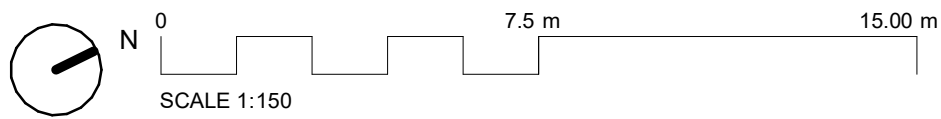

Copyright Hawkins\Brown Architects
No implied licence exists. This drawing should not be used to calculate areas for the purposes of valuation. Do not scale this drawing. All dimensions to be checked on the site by the contractor and such dimensions to be their responsibility. All work must comply with relevant British Standards and Building Regulations requirements. Drawing errors and omissions to be reported to the architect. To be read in conjunction with Architect's specification and other consultant information.

Rev	Description	Date
P1	Planning	07.12.22
P2	Update	19.12.22

Wall Key

- Existing Wall
- Proposed Wall

159 St John Street
London EC1V 4QJ

mail@hawkinsbrown.com
hawkinsbrown.com

Hawkins\Brown

Project
LSE Old Building Refurbishment
Houghton St
London WC2A 2AE
UK

Drawing
Proposed Plan Level Roof

Scale @ A1 1 : 150		Date 07/12/22
Drawn By CG		Checked By RG
Job Number 210224	Status S2	Purpose of Issue For Approval

Drawing No.
LSEOLD-HBA-V1-R1-DR-A-080160 P2

Rev