



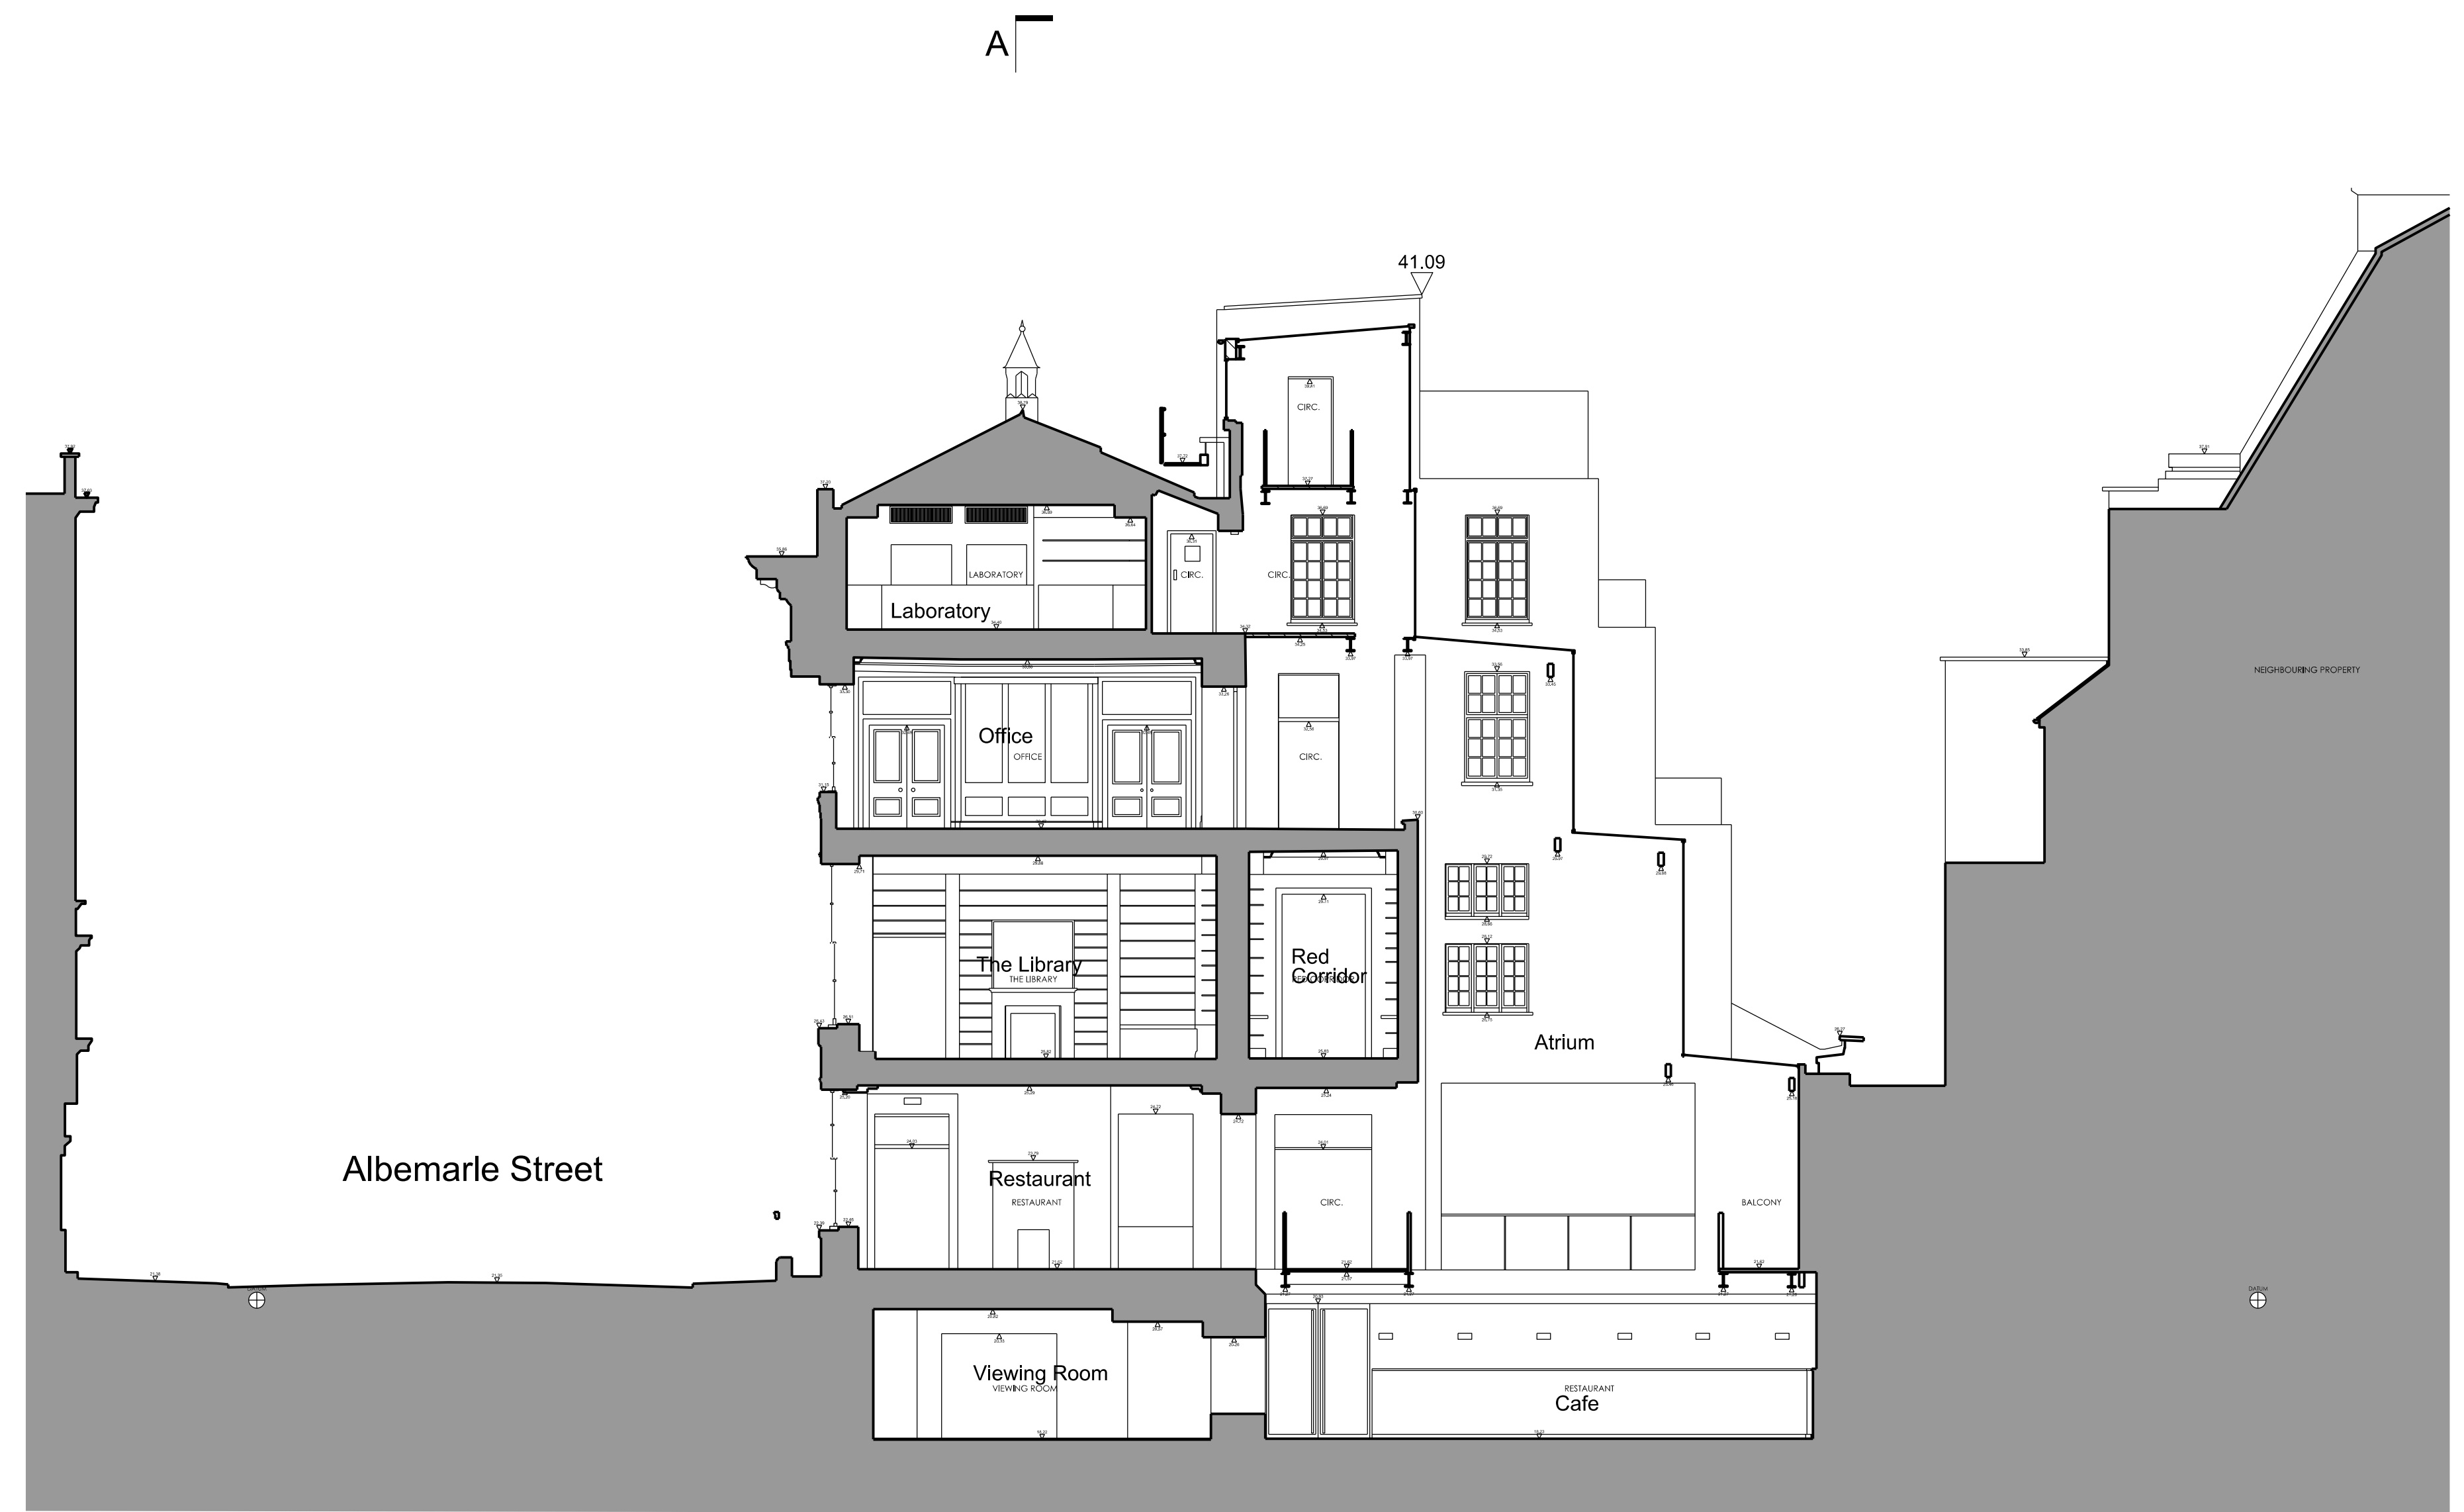

EXISTING SECTION B-B
1:100

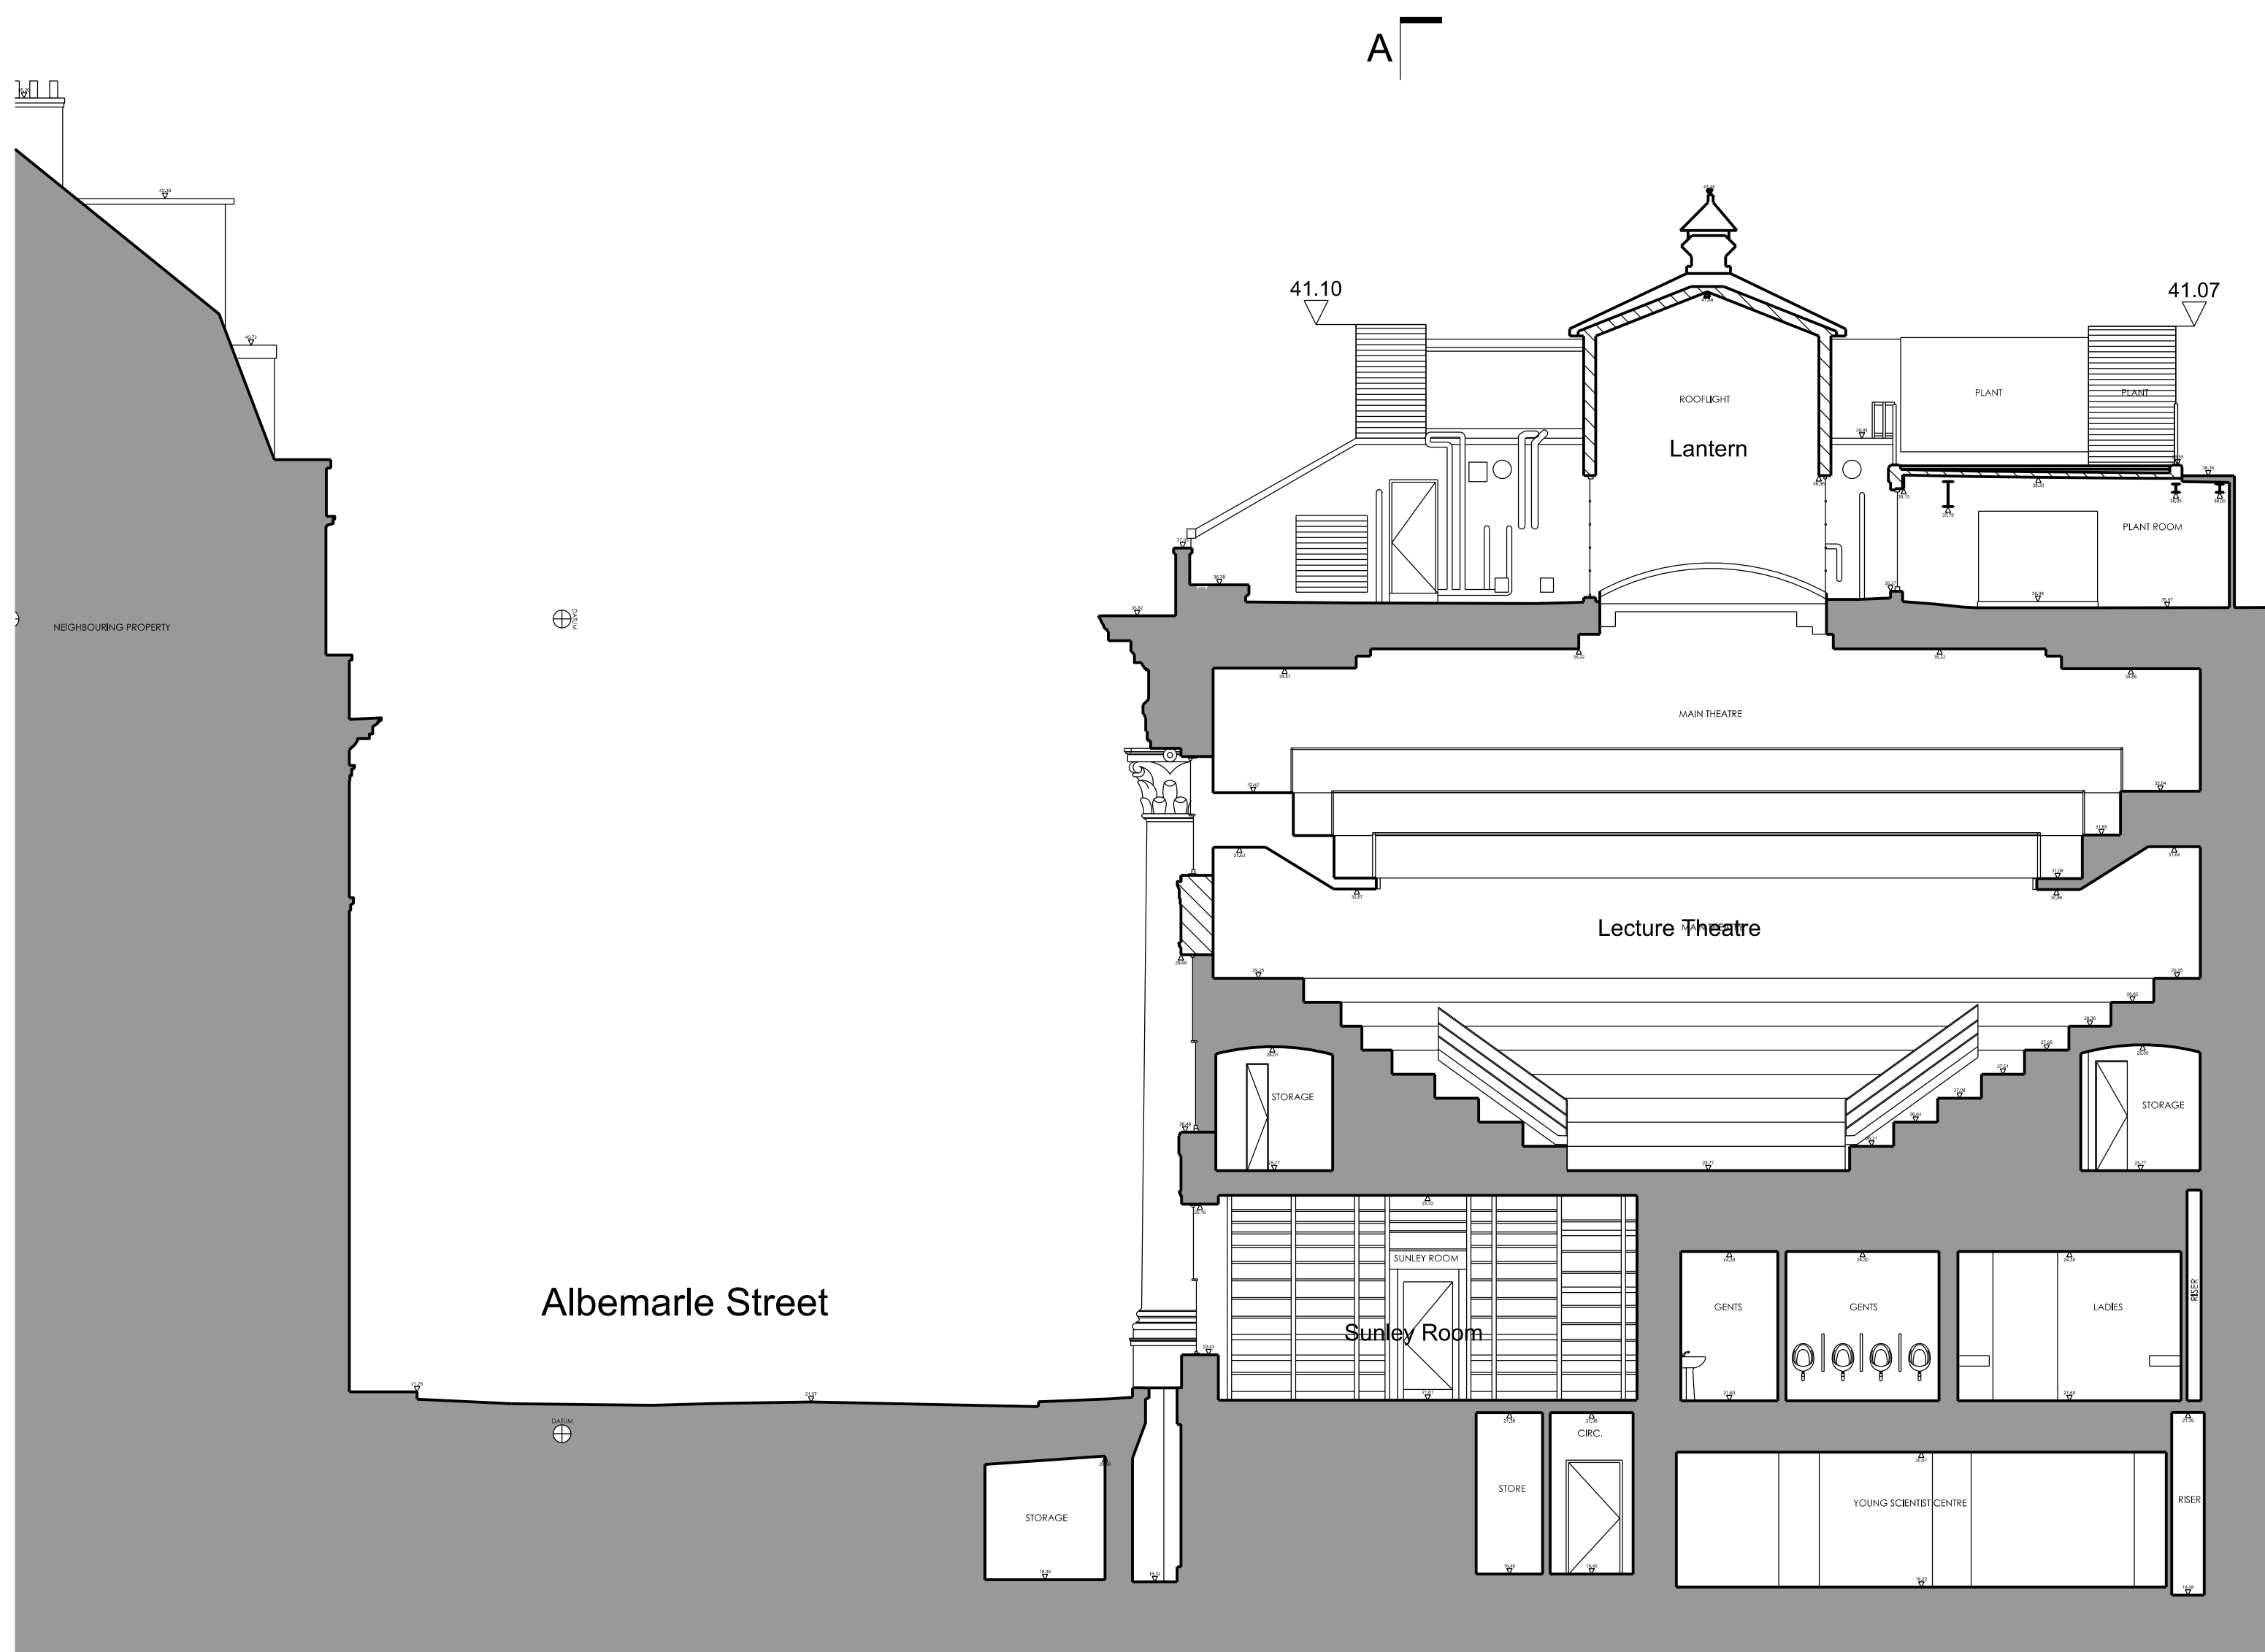

EXISTING SECTION D-D
1:100



EXISTING SECTION C-C
1:100



EXISTING SECTION E-E
1:100

BUILDING DESIGN PARTNERSHIP LTD SHALL HAVE NO RESPONSIBILITY FOR ANY USE MADE OF THIS DOCUMENT OTHER THAN THAT FOR WHICH IT WAS PREPARED AND ISSUED.

ALL DIMENSIONS SHOULD BE CHECKED ON SITE.
DO NOT SCALE FROM THIS DRAWING.

ANY DRAWING ERRORS OR DISCREPANCIES SHOULD BE BROUGHT TO THE ATTENTION OF BUILDING DESIGN PARTNERSHIP LTD AT THE ADDRESS SHOWN BELOW.

NOTES

NOTE: All site dimensions require final site survey.

Based on measured survey SOVA240415 MBS by Sovo.

Drawing to be read in conjunction with all associated BDP Significance Plans, specification and information, and Harley Haddow (BSE) and Price & Myers (C+S) information.

Key:

S Stair
L Lift

W.01 Window Code
XXX Door Code

D.01
XXX

P01: PLANNING & LBC	LB	DA	28.02.25
PROJECT DESCRIPTION	DATE	DATE	DATE

KEY NOTE

The Royal Institution
21 Albemarle Street
London,
W1S 4BS

Ri The Royal Institution
Science Lives Here

BDP.

16 Brewhouse Yard
Clerkenwell
London, EC1V 4LJ
United Kingdom

T +44 (0)20 7812 8000
F +44 (0)20 7812 8399
www.bdp.com

PROJECT TITLE
THE ROYAL INSTITUTION
FOOTPRINT PROJECT

PROJECT NO.
P3003732

EXISTING CROSS SECTIONS

SCALE
1:100@A0

DATE
28.02.2025

DRAWN
00as001

CHECKED
P01