

BUILDING DESIGN PARTNERSHIP LTD SHALL HAVE NO RESPONSIBILITY FOR ANY USE MADE OF THIS DOCUMENT OTHER THAN FOR THAT WHICH IT WAS PREPARED AND ISSUED.
ALL DIMENSIONS SHOULD BE CHECKED ON SITE.
DO NOT SCALE FROM THIS DRAWING.
ANY DRAWING ERRORS OR DISCREPANCIES SHOULD BE BROUGHT TO THE ATTENTION OF BUILDING DESIGN PARTNERSHIP LTD AT THE ADDRESS SHOWN BELOW.

NOTES


NOTE: All site dimensions require final site survey.

Based on measured survey
SOVA240415 MBS by Sovo.


Drawing to be read in conjunction
with all associated BDP Significance
Plans, specification and information,
and Harley Haddow (BSE) and Price &
Myers (C+S) information.

Key:

- S Stair
L Lift
W.01 Window Code
XXX
D.01 Door Code
XXX

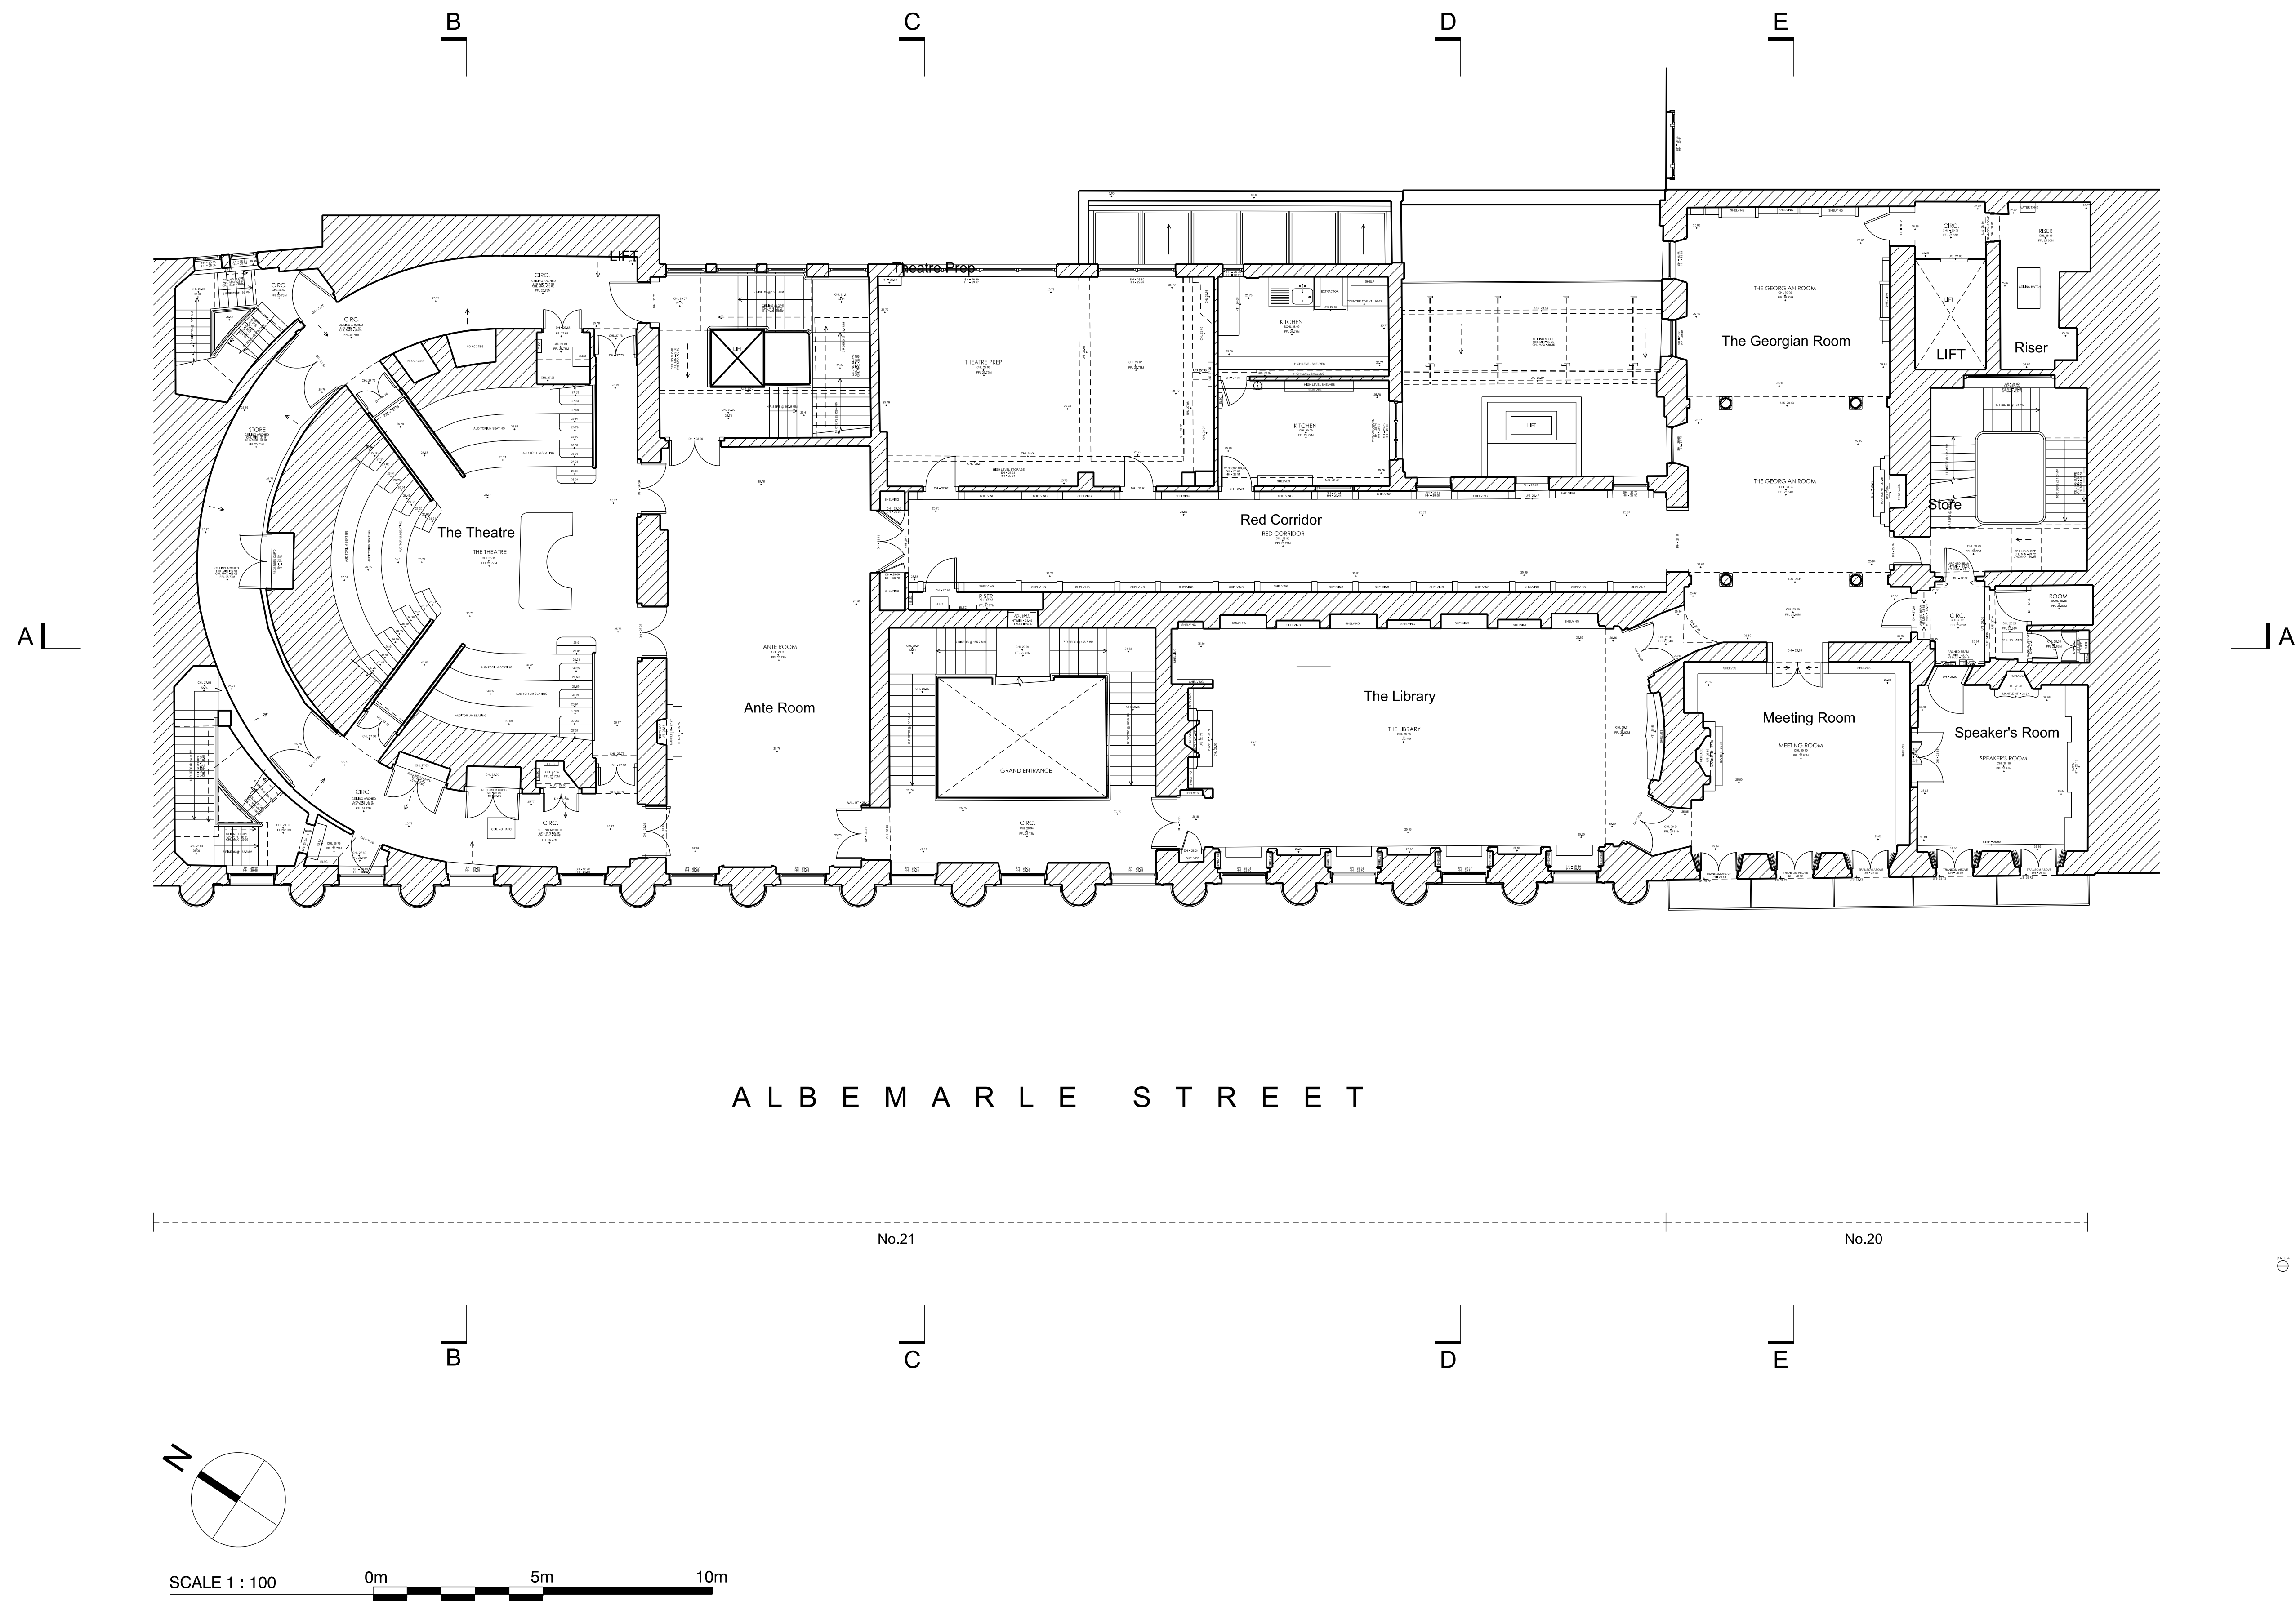

P01: PLANNING & LBC	LB	DA	28.02.25
DESIGN	DATE	DATE	DATE

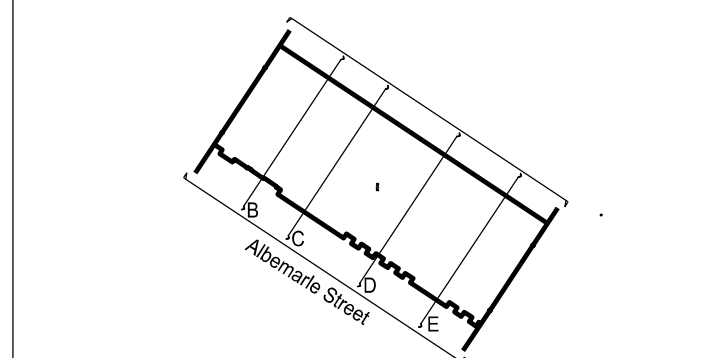

The Royal Institution
21 Albemarle Street
London,
W1S 4BS



BDP.
16 Brewhouse Yard
Clerkenwell
London, EC1V 4LJ
United Kingdom
T +44 (0)20 7812 8000
F +44 (0)20 7812 8399
www.bdp.com

PROJECT TITLE	THE ROYAL INSTITUTION FOOTPRINT PROJECT
PROJECT NO.	P3003732
PROJECT NAME	EXISTING FIRST FLOOR PLAN
SCALE	1:100@A0
DATE	28.02.2025
DESIGNER	00ap001
PROJECT	P01