



05

A

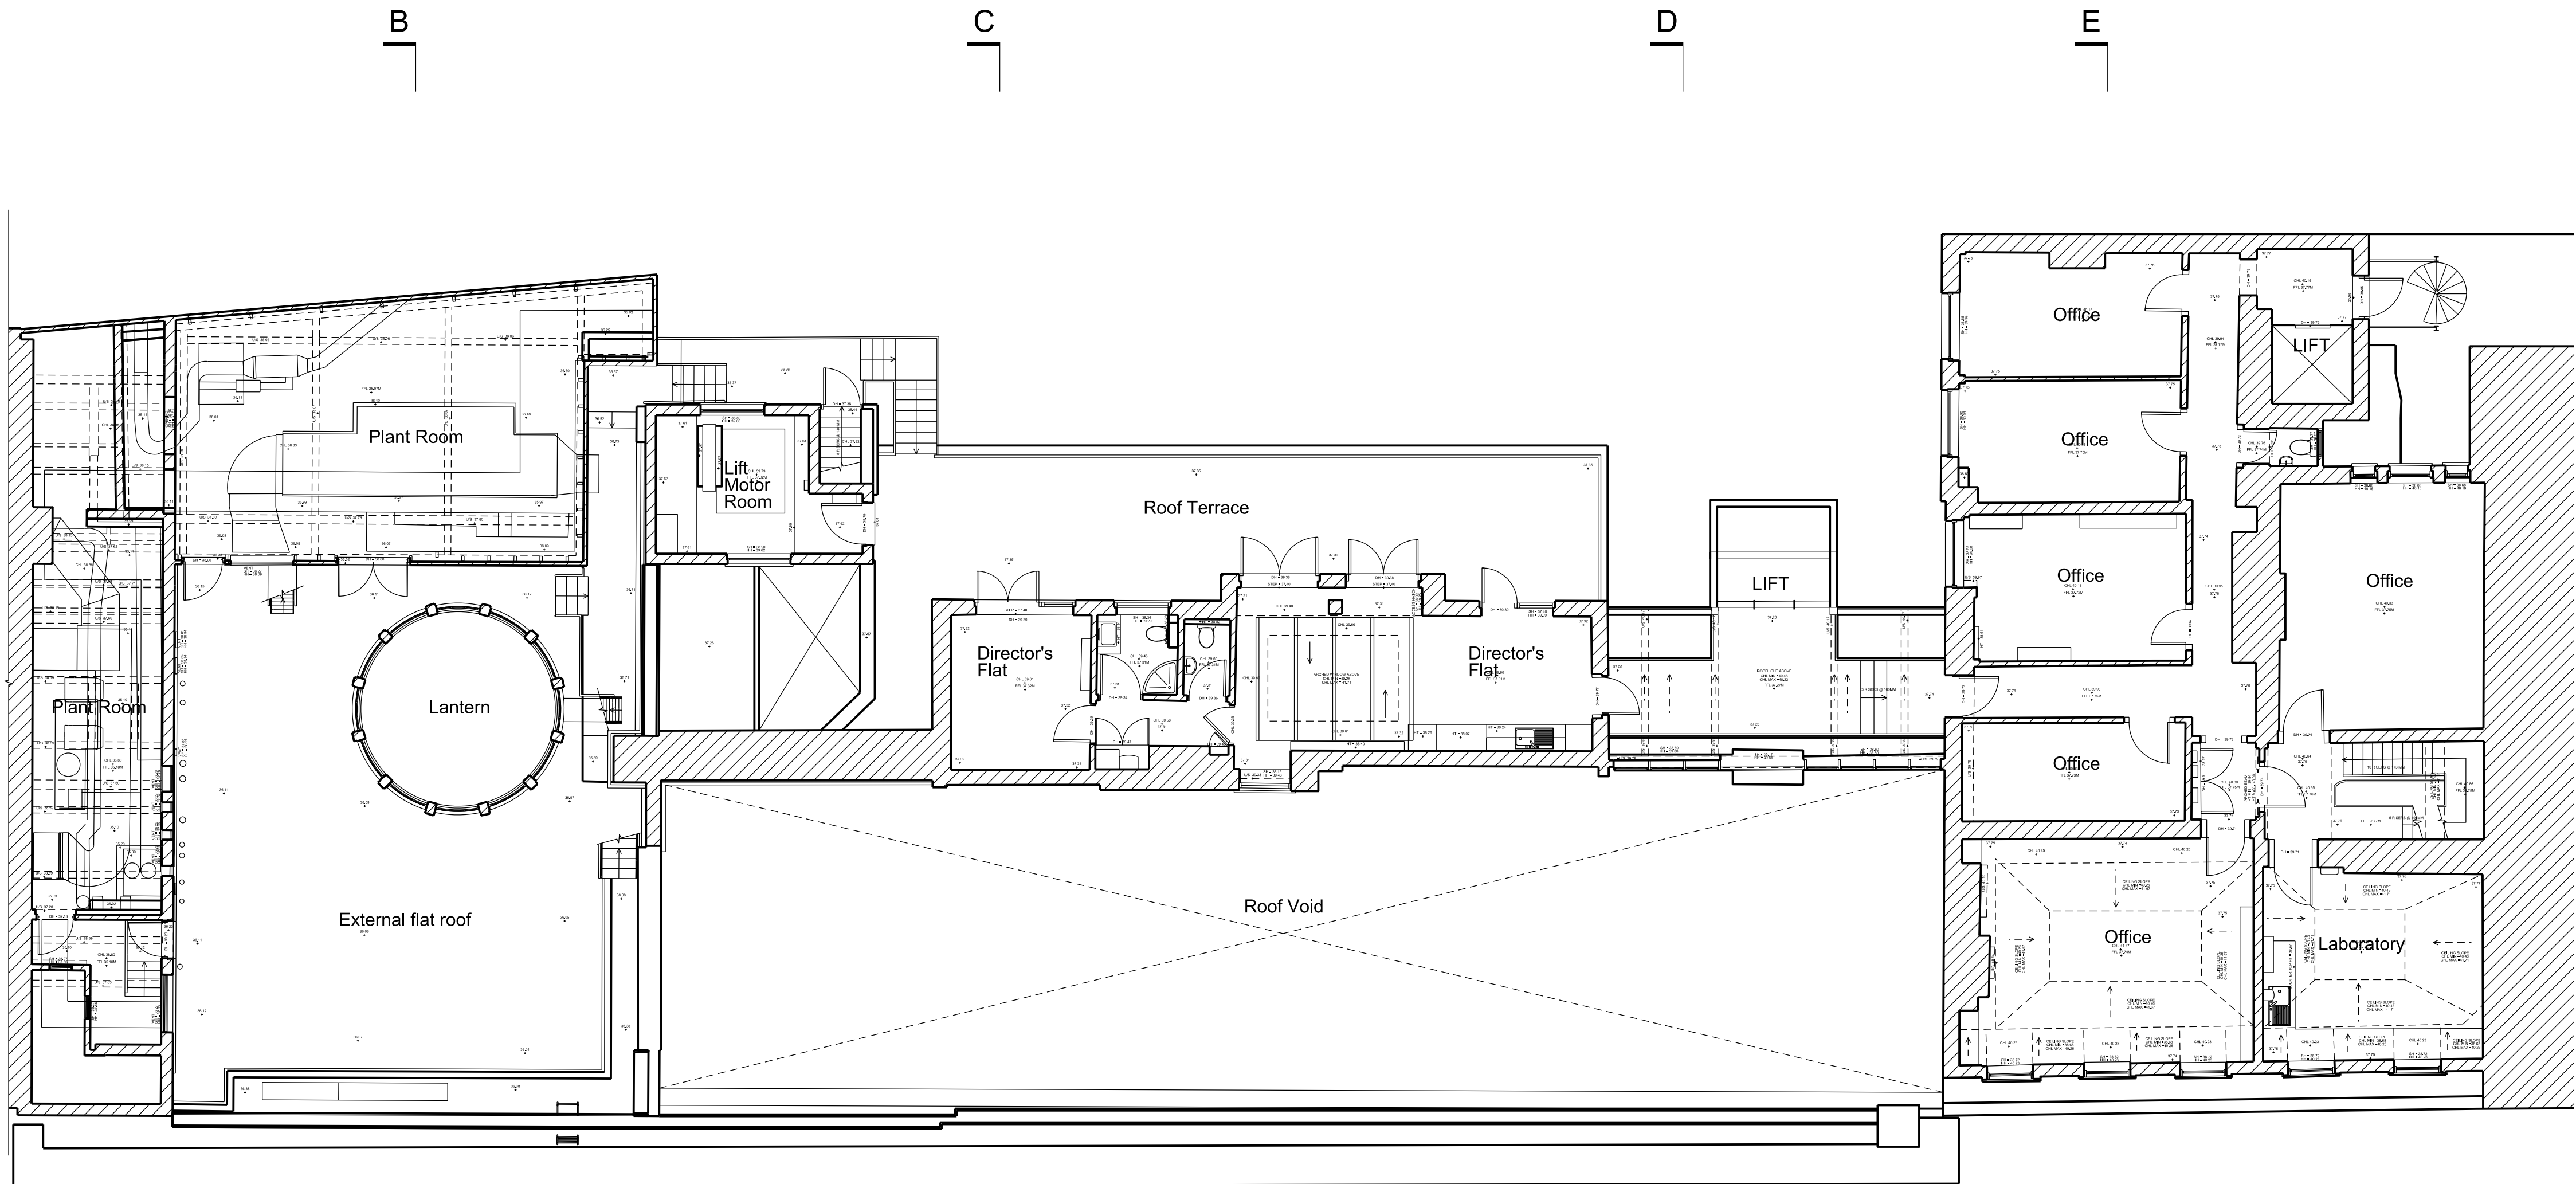

ALBEMARLE STREET

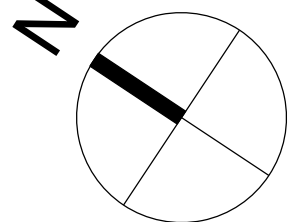

SCALE 1 : 100 0m 5m 10m

EXISTING FOURTH FLOOR PLAN
1:100

equipment room to room
information

BUILDING DESIGN PARTNERSHIP LTD SHALL HAVE NO RESPONSIBILITY FOR ANY
USE MADE OF THIS DOCUMENT OTHER THAN FOR THAT WHICH IT WAS PREPARED
AND ISSUED.
ALL DIMENSIONS SHOULD BE CHECKED ON SITE.
DO NOT SCALE FROM THIS DRAWING.
ANY DRAWING ERRORS OR DISCREPANCIES SHOULD BE BROUGHT TO THE
ATTENTION OF BUILDING DESIGN PARTNERSHIP LTD AT THE ADDRESS SHOWN
BELOW.

NOTES

NOTE: All site dimensions require final
site survey.


Based on measured survey
SOVA240415 MBS by Sovia.

Drawing to be read in conjunction
with all associated BDP Significance
Plans, specification and information,
and Harley Haddow (BSE) and Price &
Myers (C+S) information.

Key:

- S Stair
- L Lift
- W.01 Window Code
- XXX Door Code

P01: PLANNING & LBC	LB	DA 28.02.25
PROJECT DESCRIPTION	DATE	DATE

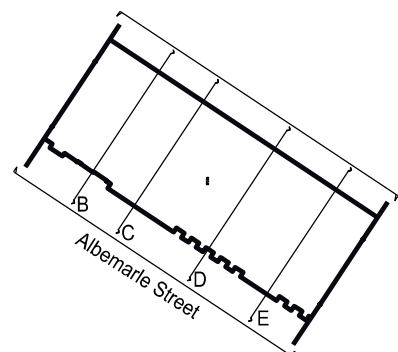

Client Name
The Royal Institution
21 Albemarle Street
London,
W1S 4BS



BDP.

16 Brewhouse Yard
Clerkenwell
London, EC1V 4LJ
United Kingdom
T +44 (0)20 7812 8000
F +44 (0)20 7812 8399
www.bdp.com

PROJECT TITLE THE ROYAL INSTITUTION FOOTPRINT PROJECT	SCALE 1:100@A0
PROJECT NO. P3003732	DATE 28.02.2025
EXISTING FOURTH FLOOR PLAN	REVISION P01