

BUILDING DESIGN PARTNERSHIP LTD SHALL HAVE NO RESPONSIBILITY FOR ANY USE MADE OF THIS DOCUMENT OTHER THAN FOR THAT WHICH IT WAS PREPARED AND ISSUED.
ALL DIMENSIONS SHOULD BE CHECKED ON SITE.
DO NOT SCALE FROM THIS DRAWING.
ANY DRAWING ERRORS OR DISCREPANCIES SHOULD BE BROUGHT TO THE ATTENTION OF BUILDING DESIGN PARTNERSHIP LTD AT THE ADDRESS SHOWN BELOW.

NOTES

NOTE: All site dimensions require final site survey.

Based on measured survey
SOVA240415 MBS by Sovia.

Drawing to be read in conjunction
with all associated BDP Significance
Plans, specification and information,
and Harley Haddow (BSE) and Price &
Myers (C+S) information.


Key:

- S


L
- Stair
Lift
- W.01

XXX
- Window Code
- D.01

XXX
- Door Code

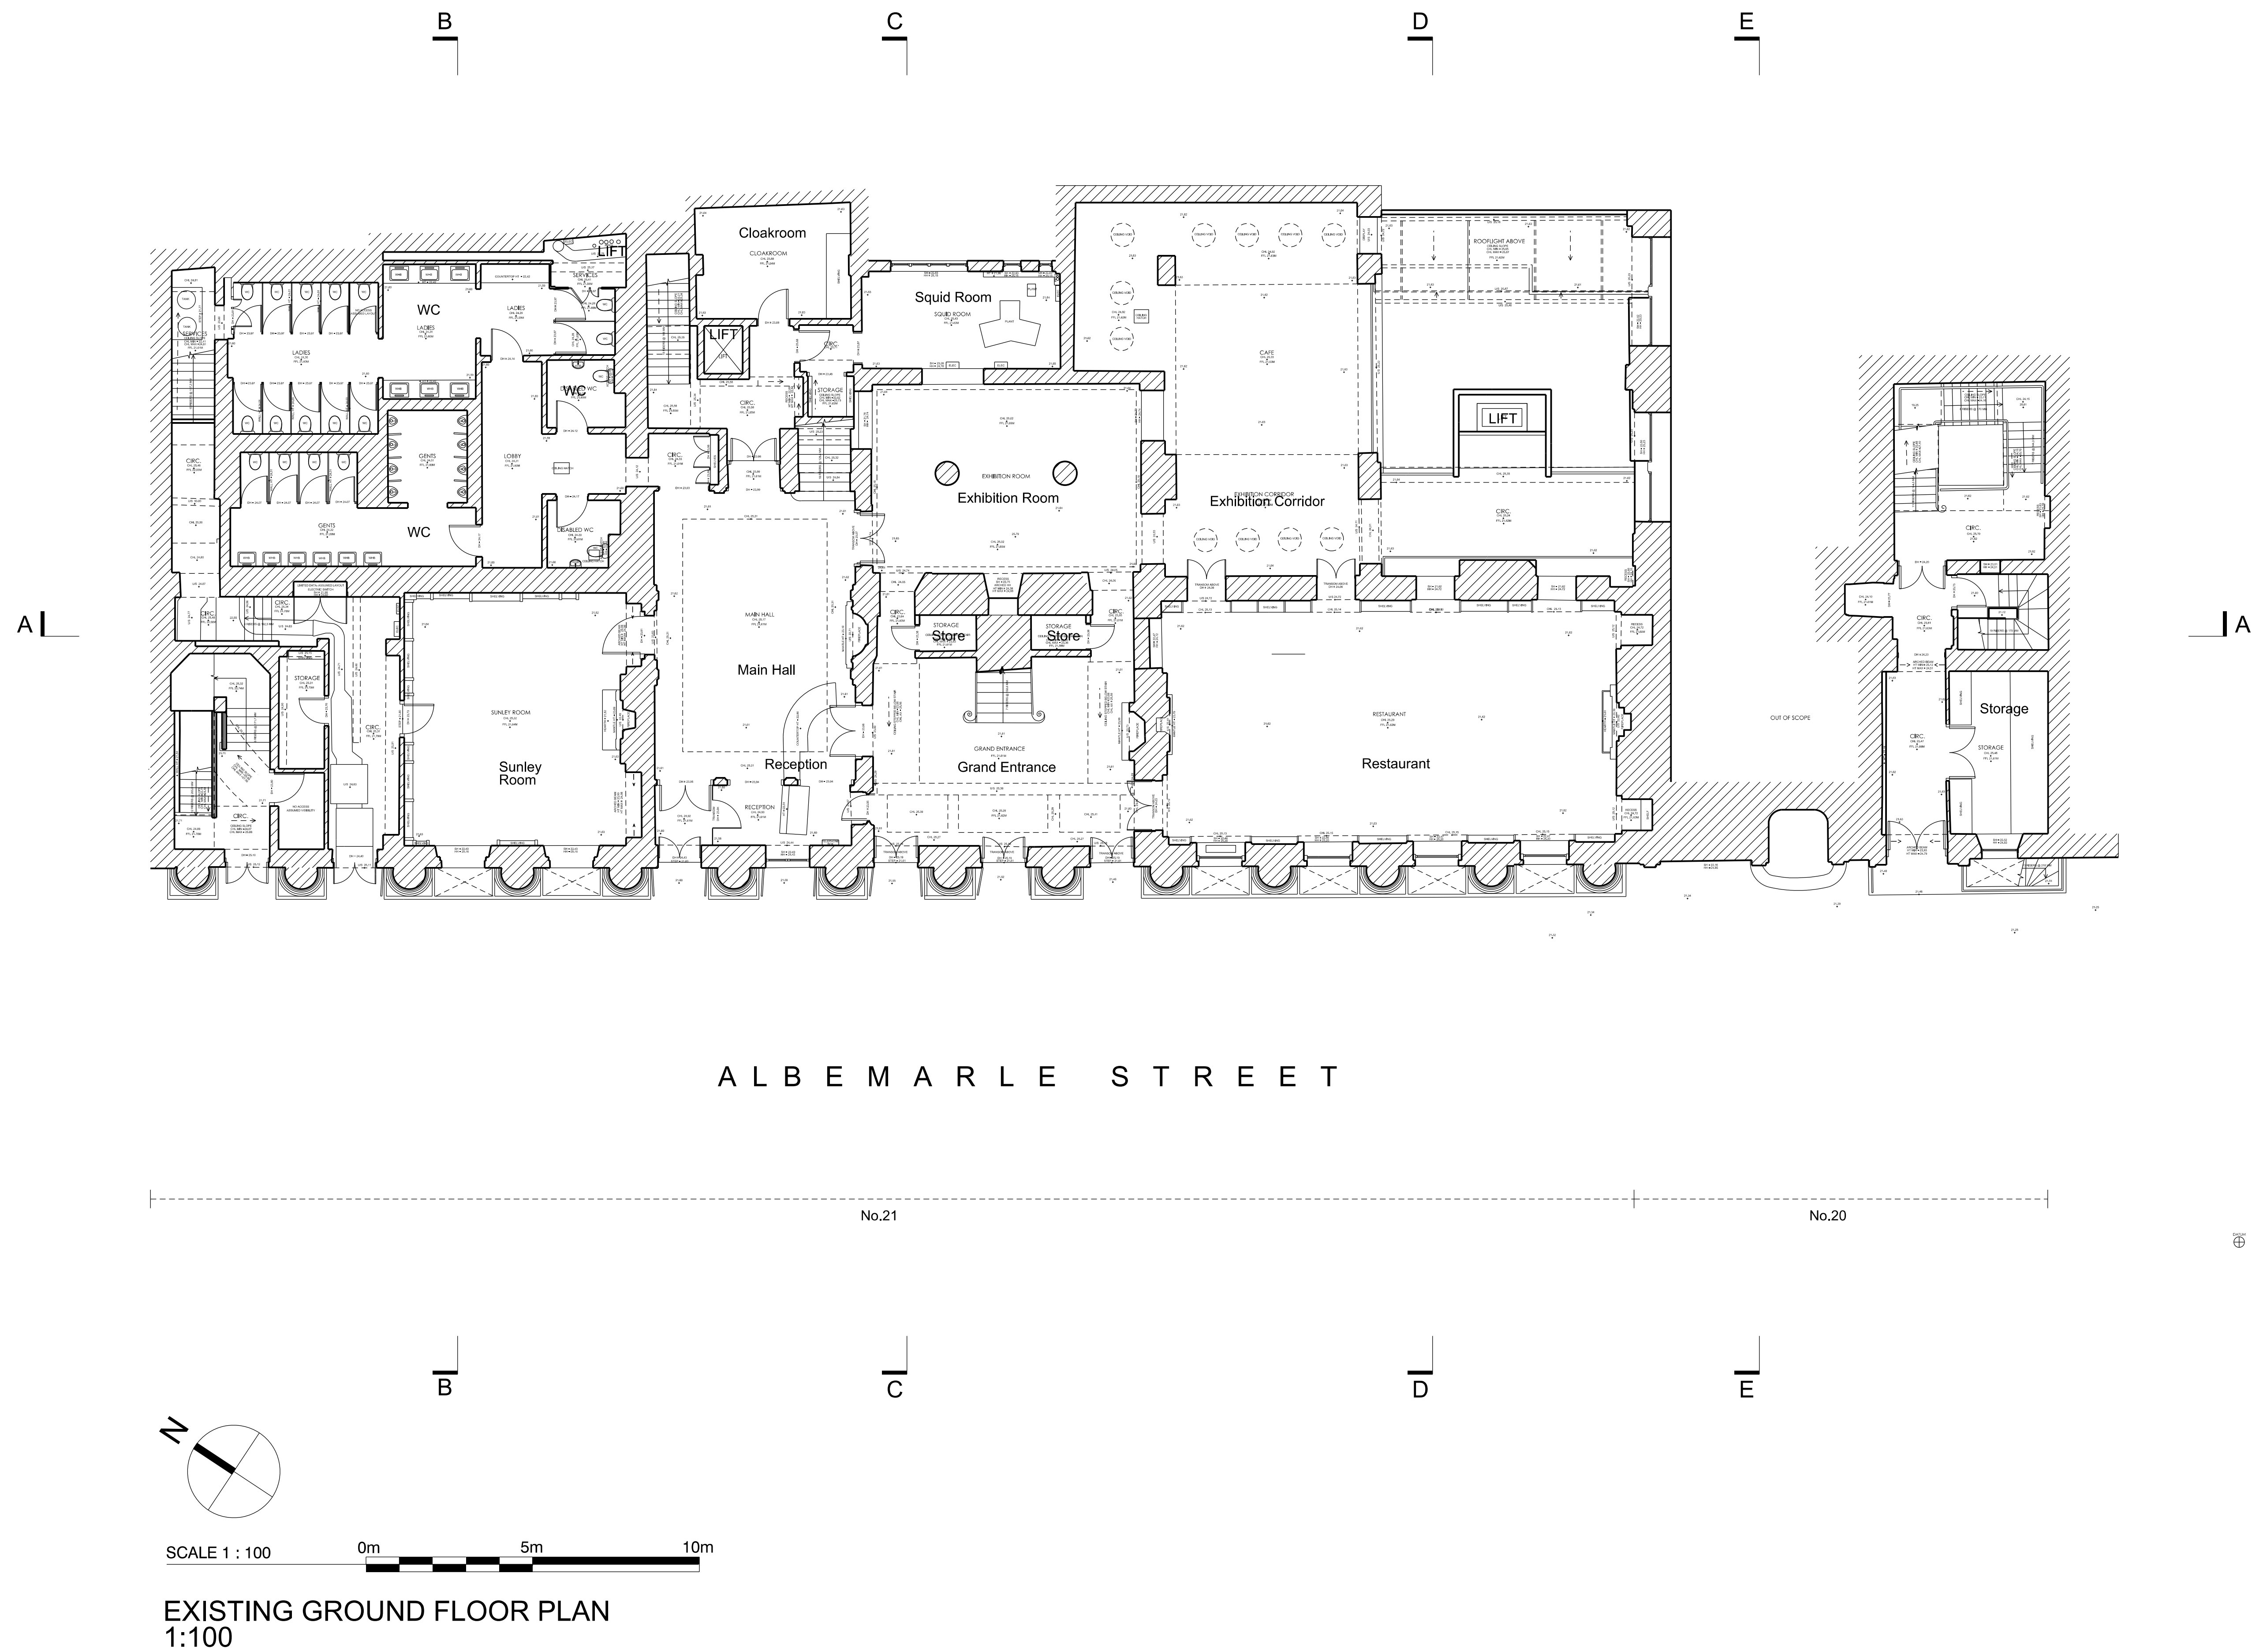

P01: PLANNING & LBC	LB	DA 28.02.25
DESIGN REVISION	DATE	BY

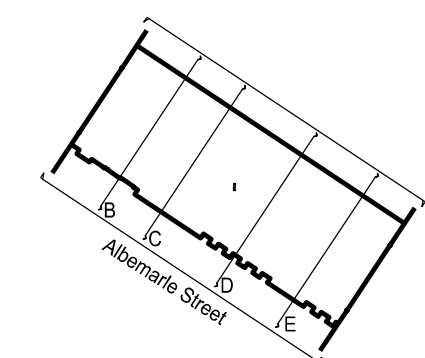

Client Name:
The Royal Institution
21 Albemarle Street
London,
W1S 4BS



BDP.

16 Brewhouse Yard
Clerkenwell
London, EC1V 4LJ
United Kingdom
T +44 (0)20 7812 8000
F +44 (0)20 7812 8399
www.bdp.com

PROJECT TITLE THE ROYAL INSTITUTION FOOTPRINT PROJECT	
PROJECT NO. P3003732	
PROJECT NAME EXISTING GROUND FLOOR PLAN	SCALE 1:100@A0
DATE 28.02.2025	
DRAWN BY 00ap001	CHECKED BY P01