


05

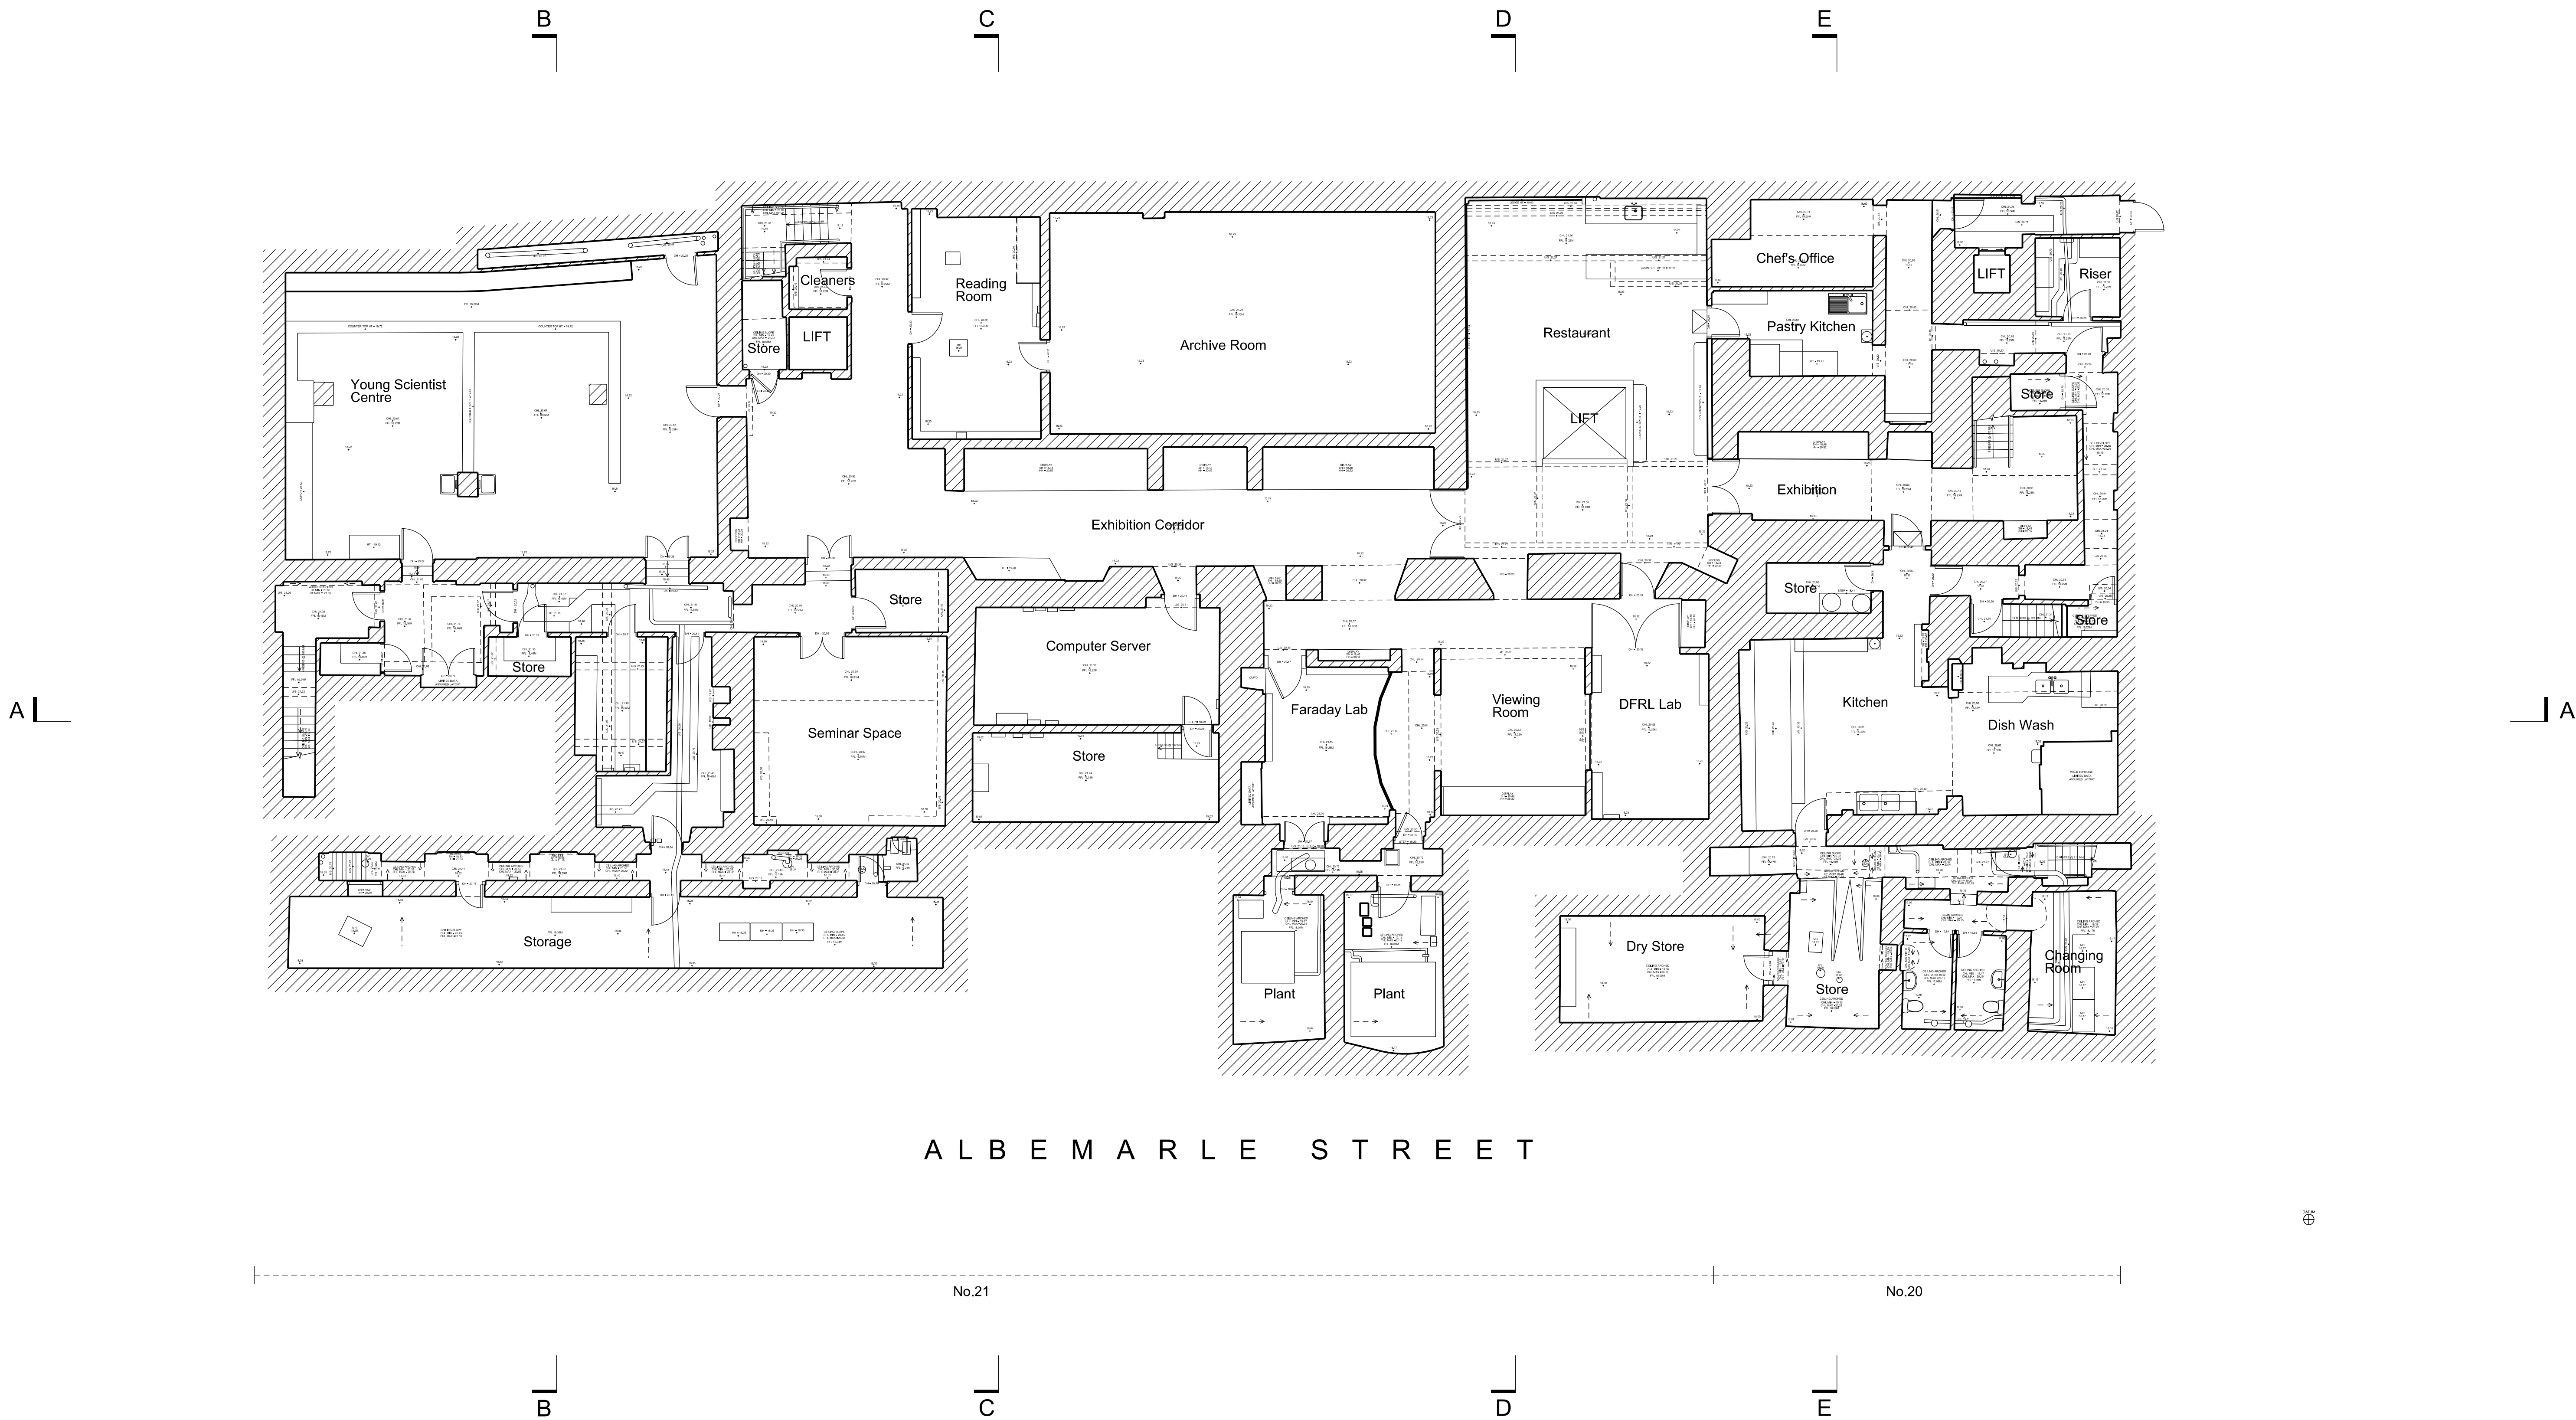

SCALE 1 : 100
0m 5m 10m
EXISTING LOWER GROUND FLOOR PLAN
1:100

BUILDING DESIGN PARTNERSHIP LTD SHALL HAVE NO RESPONSIBILITY FOR ANY USE MADE OF THIS DOCUMENT OTHER THAN FOR THAT WHICH IT WAS PREPARED AND ISSUED.
ALL DIMENSIONS SHOULD BE CHECKED ON SITE.
DO NOT SCALE FROM THIS DRAWING.
ANY DRAWING ERRORS OR DISCREPANCIES SHOULD BE BROUGHT TO THE ATTENTION OF BUILDING DESIGN PARTNERSHIP LTD AT THE ADDRESS SHOWN BELOW.

NOTES

NOTE: All site dimensions require final site survey.

Based on measured survey SOVA240415 MBS by Sovia.

Drawing to be read in conjunction with all associated BDP Significance Plans, specification and information, and Harley Haddow (BSE) and Price & Myers (C+S) information.

Key:

S Stair
L Lift

W.01 Window Code
XXX

D.01 Door Code
XXX

P01: PLANNING & LBC	LB	DA 28.02.25
DATE: 28.02.25		
The Royal Institution 21 Albemarle Street London, W1S 4BS		
16 Brewhouse Yard Clerkenwell London, EC1V 4LJ United Kingdom T +44 (0)20 7812 8000 F +44 (0)20 7812 8399 www.bdp.com		
PROJECT TITLE THE ROYAL INSTITUTION FOOTPRINT PROJECT		
PROJECT CODE P3003732		
DRAWN BY EXISTING LOWER GROUND FLOOR PLAN		
SCALE 1:100@A0		
DATE 28.02.2025		
DRAWN BY 00ap0LG		
CHECKED BY P01		

P01: PLANNING & LBC	LB	DA 28.02.25
DATE: 28.02.25		
The Royal Institution 21 Albemarle Street London, W1S 4BS		
16 Brewhouse Yard Clerkenwell London, EC1V 4LJ United Kingdom T +44 (0)20 7812 8000 F +44 (0)20 7812 8399 www.bdp.com		
PROJECT TITLE THE ROYAL INSTITUTION FOOTPRINT PROJECT		
PROJECT CODE P3003732		
DRAWN BY EXISTING LOWER GROUND FLOOR PLAN		
SCALE 1:100@A0		
DATE 28.02.2025		
DRAWN BY 00ap0LG		
CHECKED BY P01		