


WINDOWS AND DOORS SCHEDULE		
	PHASE 1	PHASE 2
DOORS	JOINERY FIXES/SEALS	SOLAR FILM
D.01.C15	●	●
D.02.C15	●	●
D.03.C15	●	●
D.01.C16	●	●
D.02.C16	●	●
WINDOWS		
W.01.S9		●
W.01.S3		●
W.02.S3		●
W.03.S3		●
W.04.S3		●
W.01.C9		●
W.02.C9		●
W.03.C10		●
W.01.C14		●
W.01.S8	●	
W.01.C4	●	
W.02.C4	●	
W.03.C4	●	
W.01.C6	●	
W.02.C6	●	
W.02.C6	●	
W.01.C12	●	
W.02.C12	●	
W.03.C12	●	
W.01.C13	●	
W.02.C13	●	
W.03.C13	●	

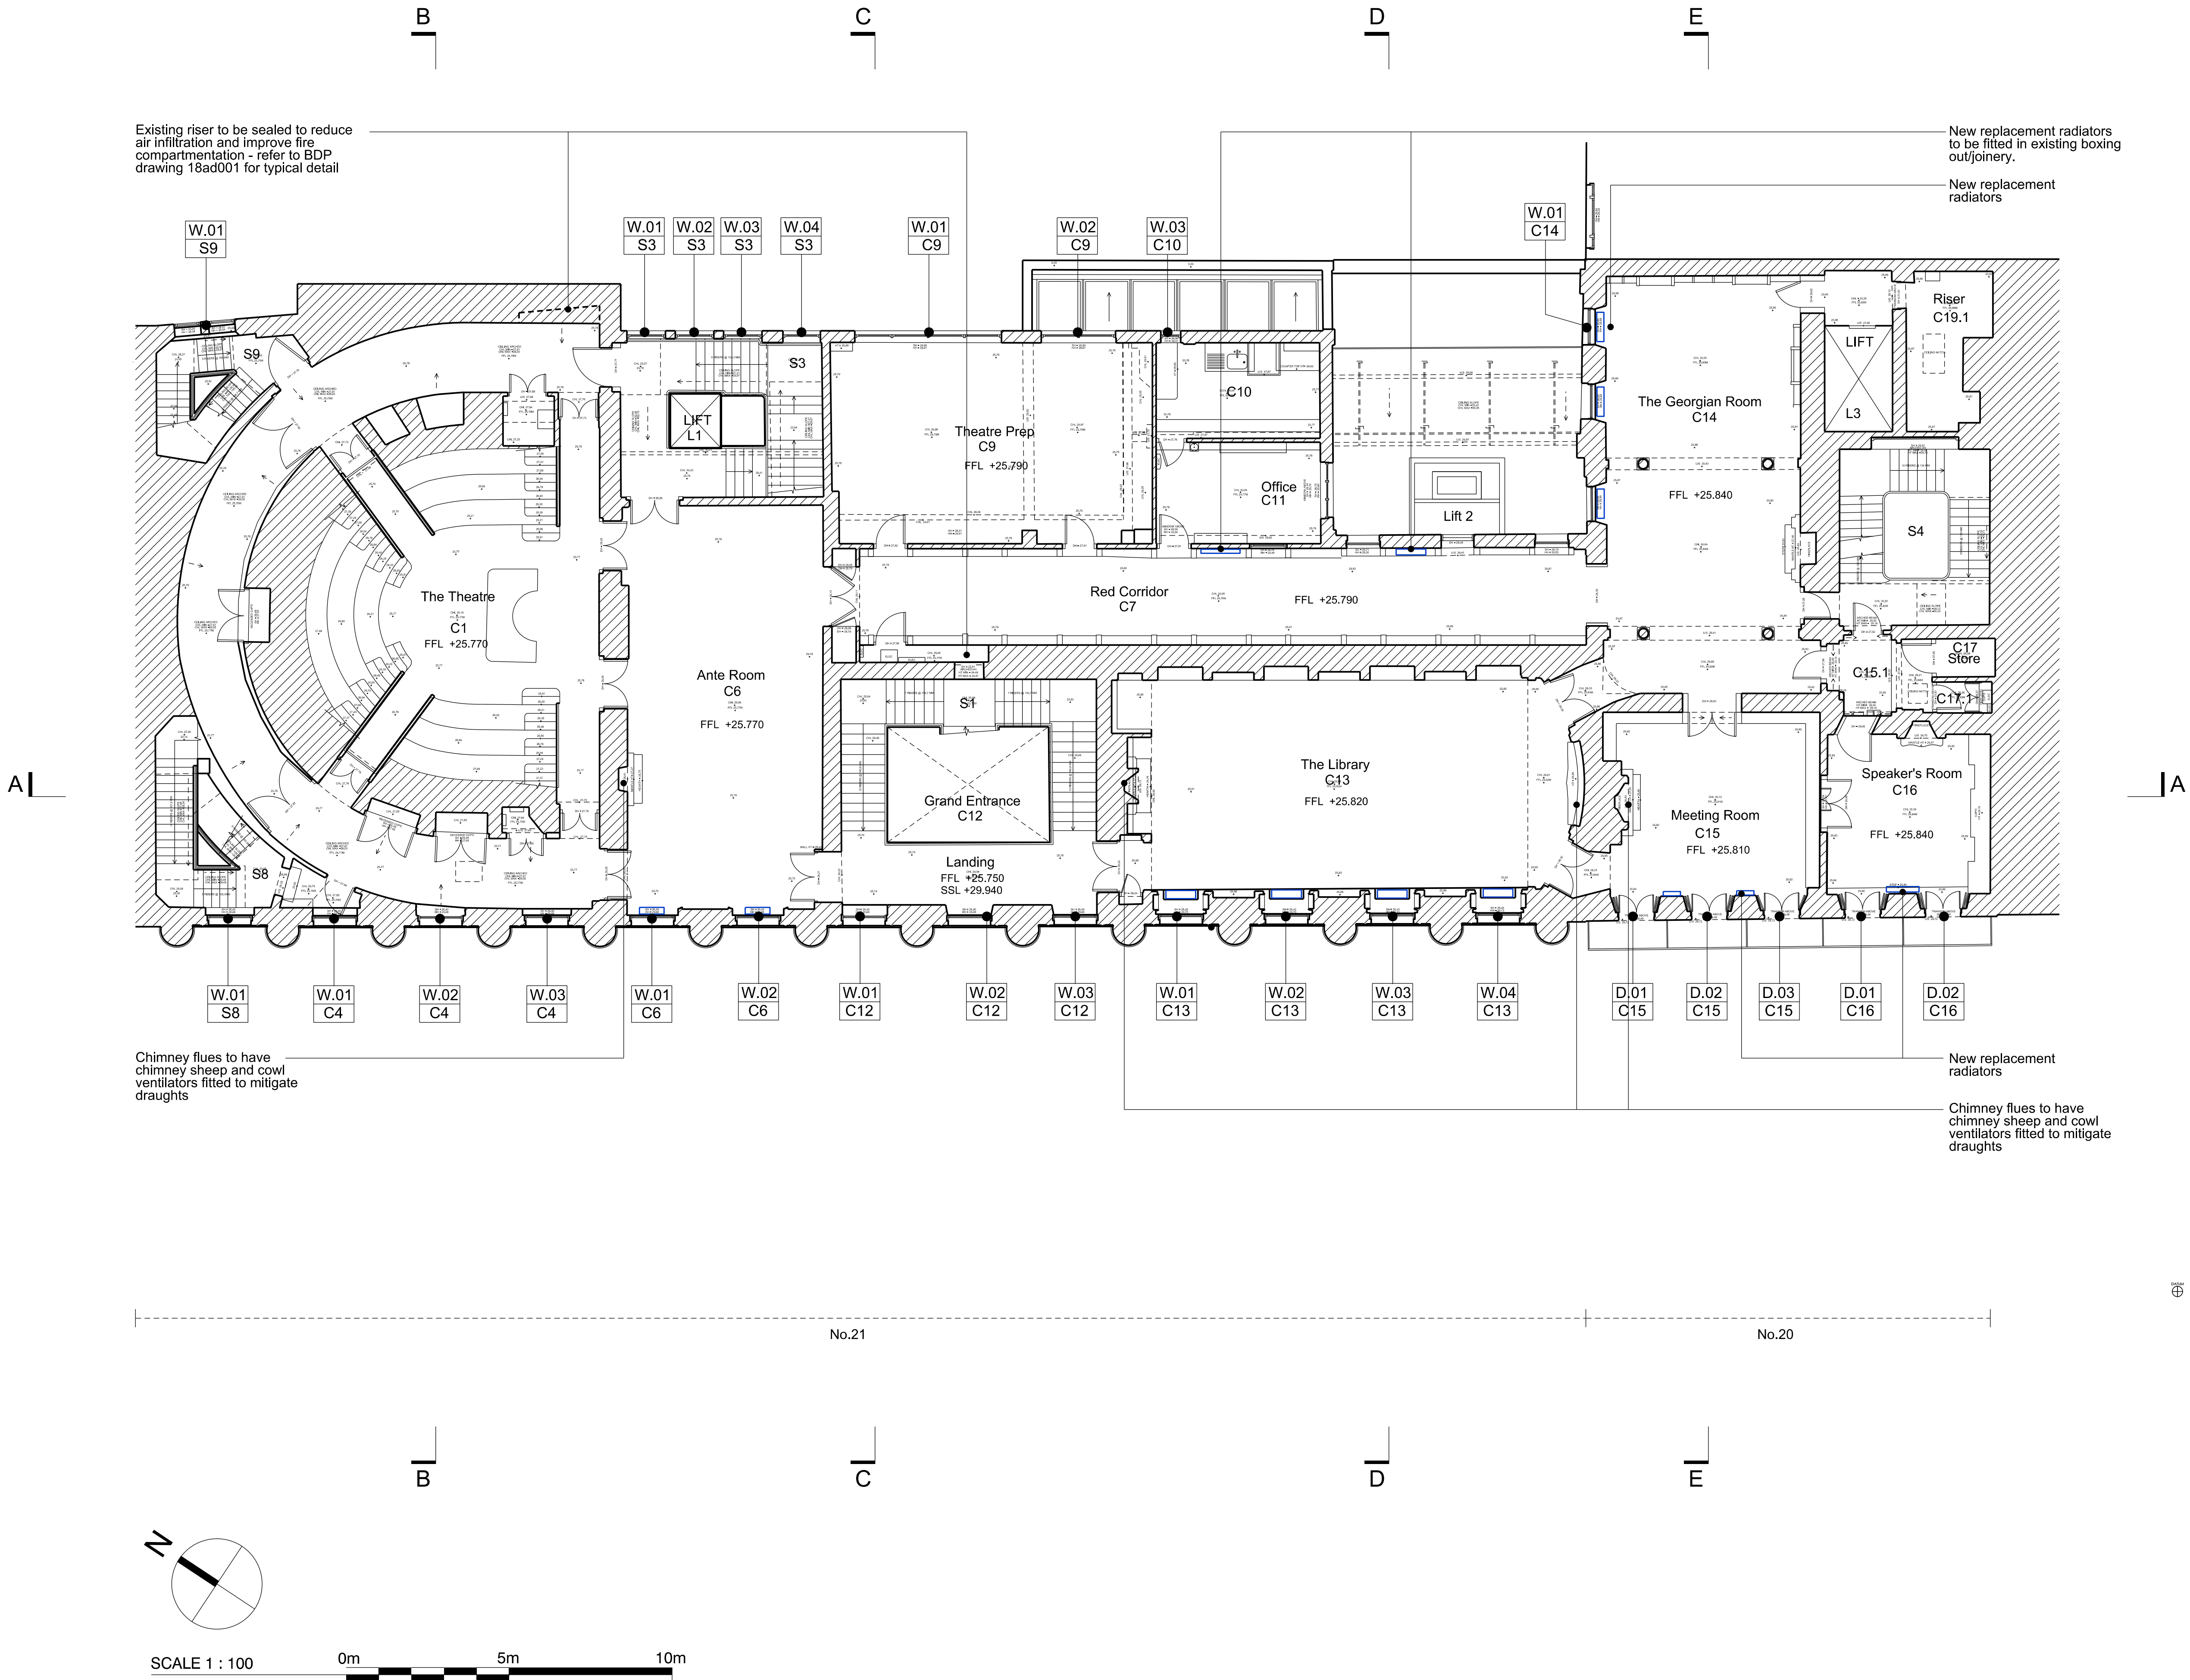

PROPOSED FIRST FLOOR PLAN
1:100

BUILDING DESIGN PARTNERSHIP LTD SHALL HAVE NO RESPONSIBILITY FOR ANY USE MADE OF THIS DOCUMENT OTHER THAN FOR THAT WHICH IT WAS PREPARED AND ISSUED.

ALL DIMENSIONS SHOULD BE CHECKED ON SITE. DO NOT SCALE FROM THIS DRAWING.

ANY DRAWING ERRORS OR DISCREPANCIES SHOULD BE BROUGHT TO THE ATTENTION OF BUILDING DESIGN PARTNERSHIP LTD AT THE ADDRESS SHOWN BELOW.

NOTES

NOTE: All site dimensions require final site survey.

Based on measured survey SOVA240415 MBS by Sova.

Drawing to be read in conjunction with all associated BDP Significance Plans, specification and information, and Harley Haddow (BSE) and Price & Myers (C+S) information.

Key:

S

L

Window Code

Door Code

Project proposals

P01: PLANNING & LBC	LB	DA 28.02.25
DATE	DATE	DATE

Client Name

The Royal Institution
21 Albemarle Street
London,
W1S 4BS

The Royal Institution
Science Lives Here

16 Brewhouse Yard
Clerkenwell
London, EC1V 4LJ
United Kingdom

T +44 (0)20 7812 8000
F +44 (0)20 7812 8399
www.bdp.com

PROJECT TITLE	THE ROYAL INSTITUTION FOOTPRINT PROJECT
PROJECT CODE	P3003732
DOCUMENT TITLE	PROPOSED FIRST FLOOR PLAN
SCALE	1:100@A0
DATE	28.02.2025
DESIGNER	20ap001
PROJECT	P01